





	1	2	3	4	5	6	7	8	9	10	11	12	13	14	15	16	17
A	Schemat instalacji elektrotechnicznej mikrobiogazowni Rybno																
B																	
C																	
D																	
E																	
F																	
G																	
H																	
 Autor: Mateusz Żygadło Data: 16.10.2025					Schemat instalacji elektrotechnicznej mikrobiogazowni Rybno								Plik: Arkusz: 1/29				




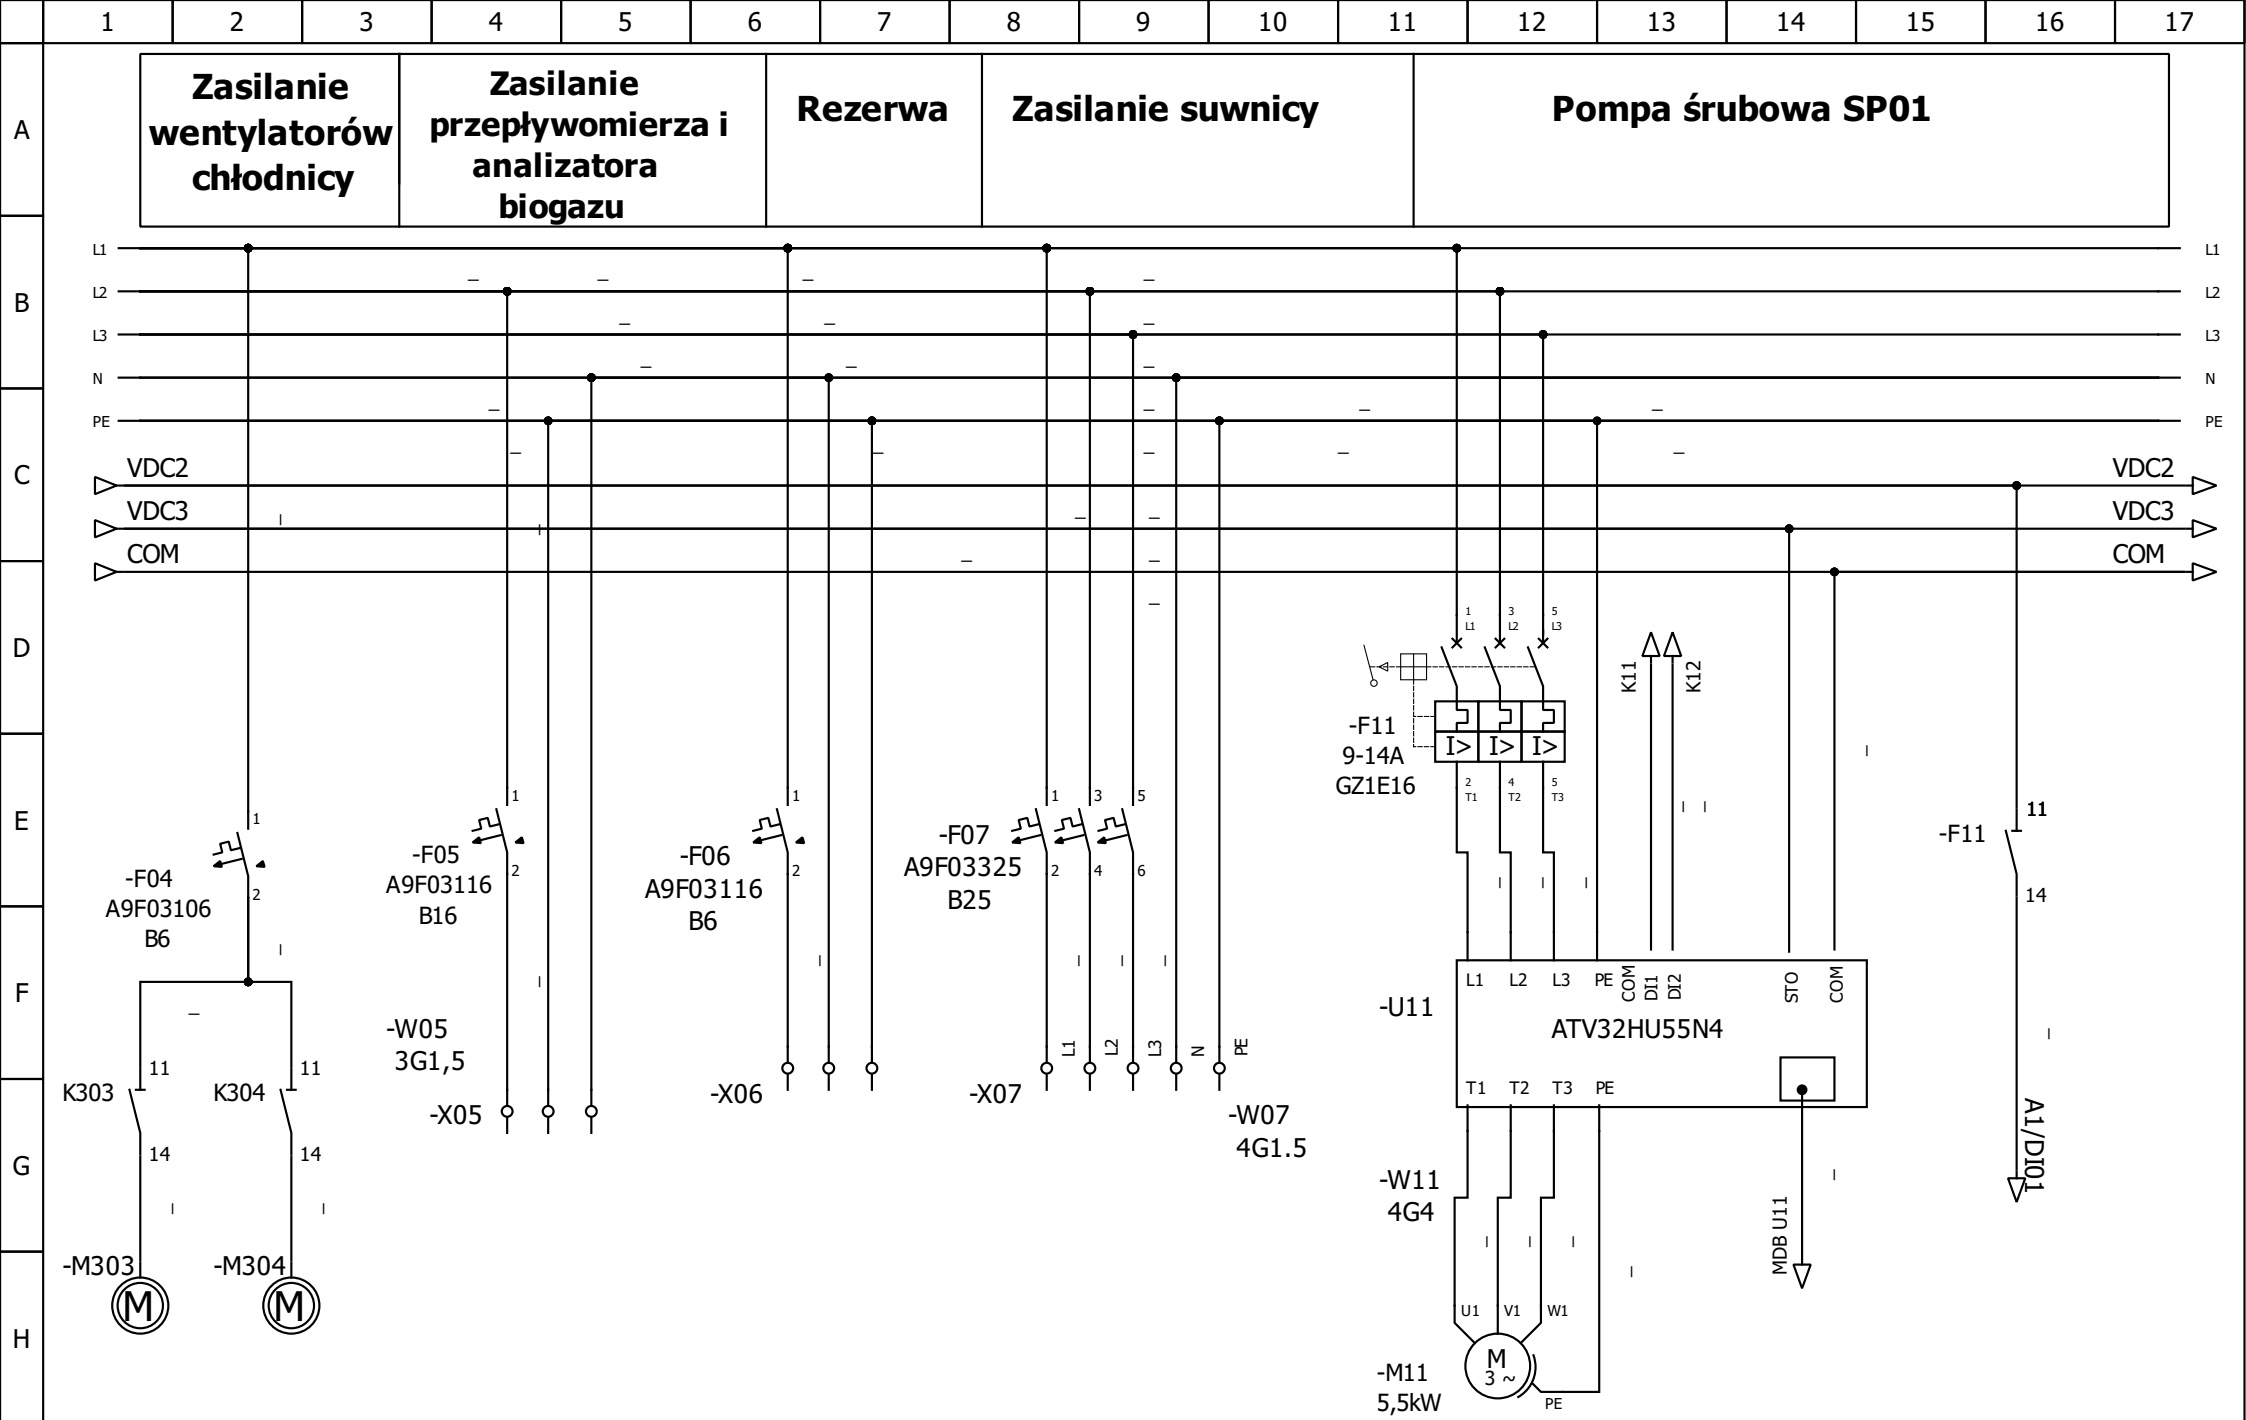


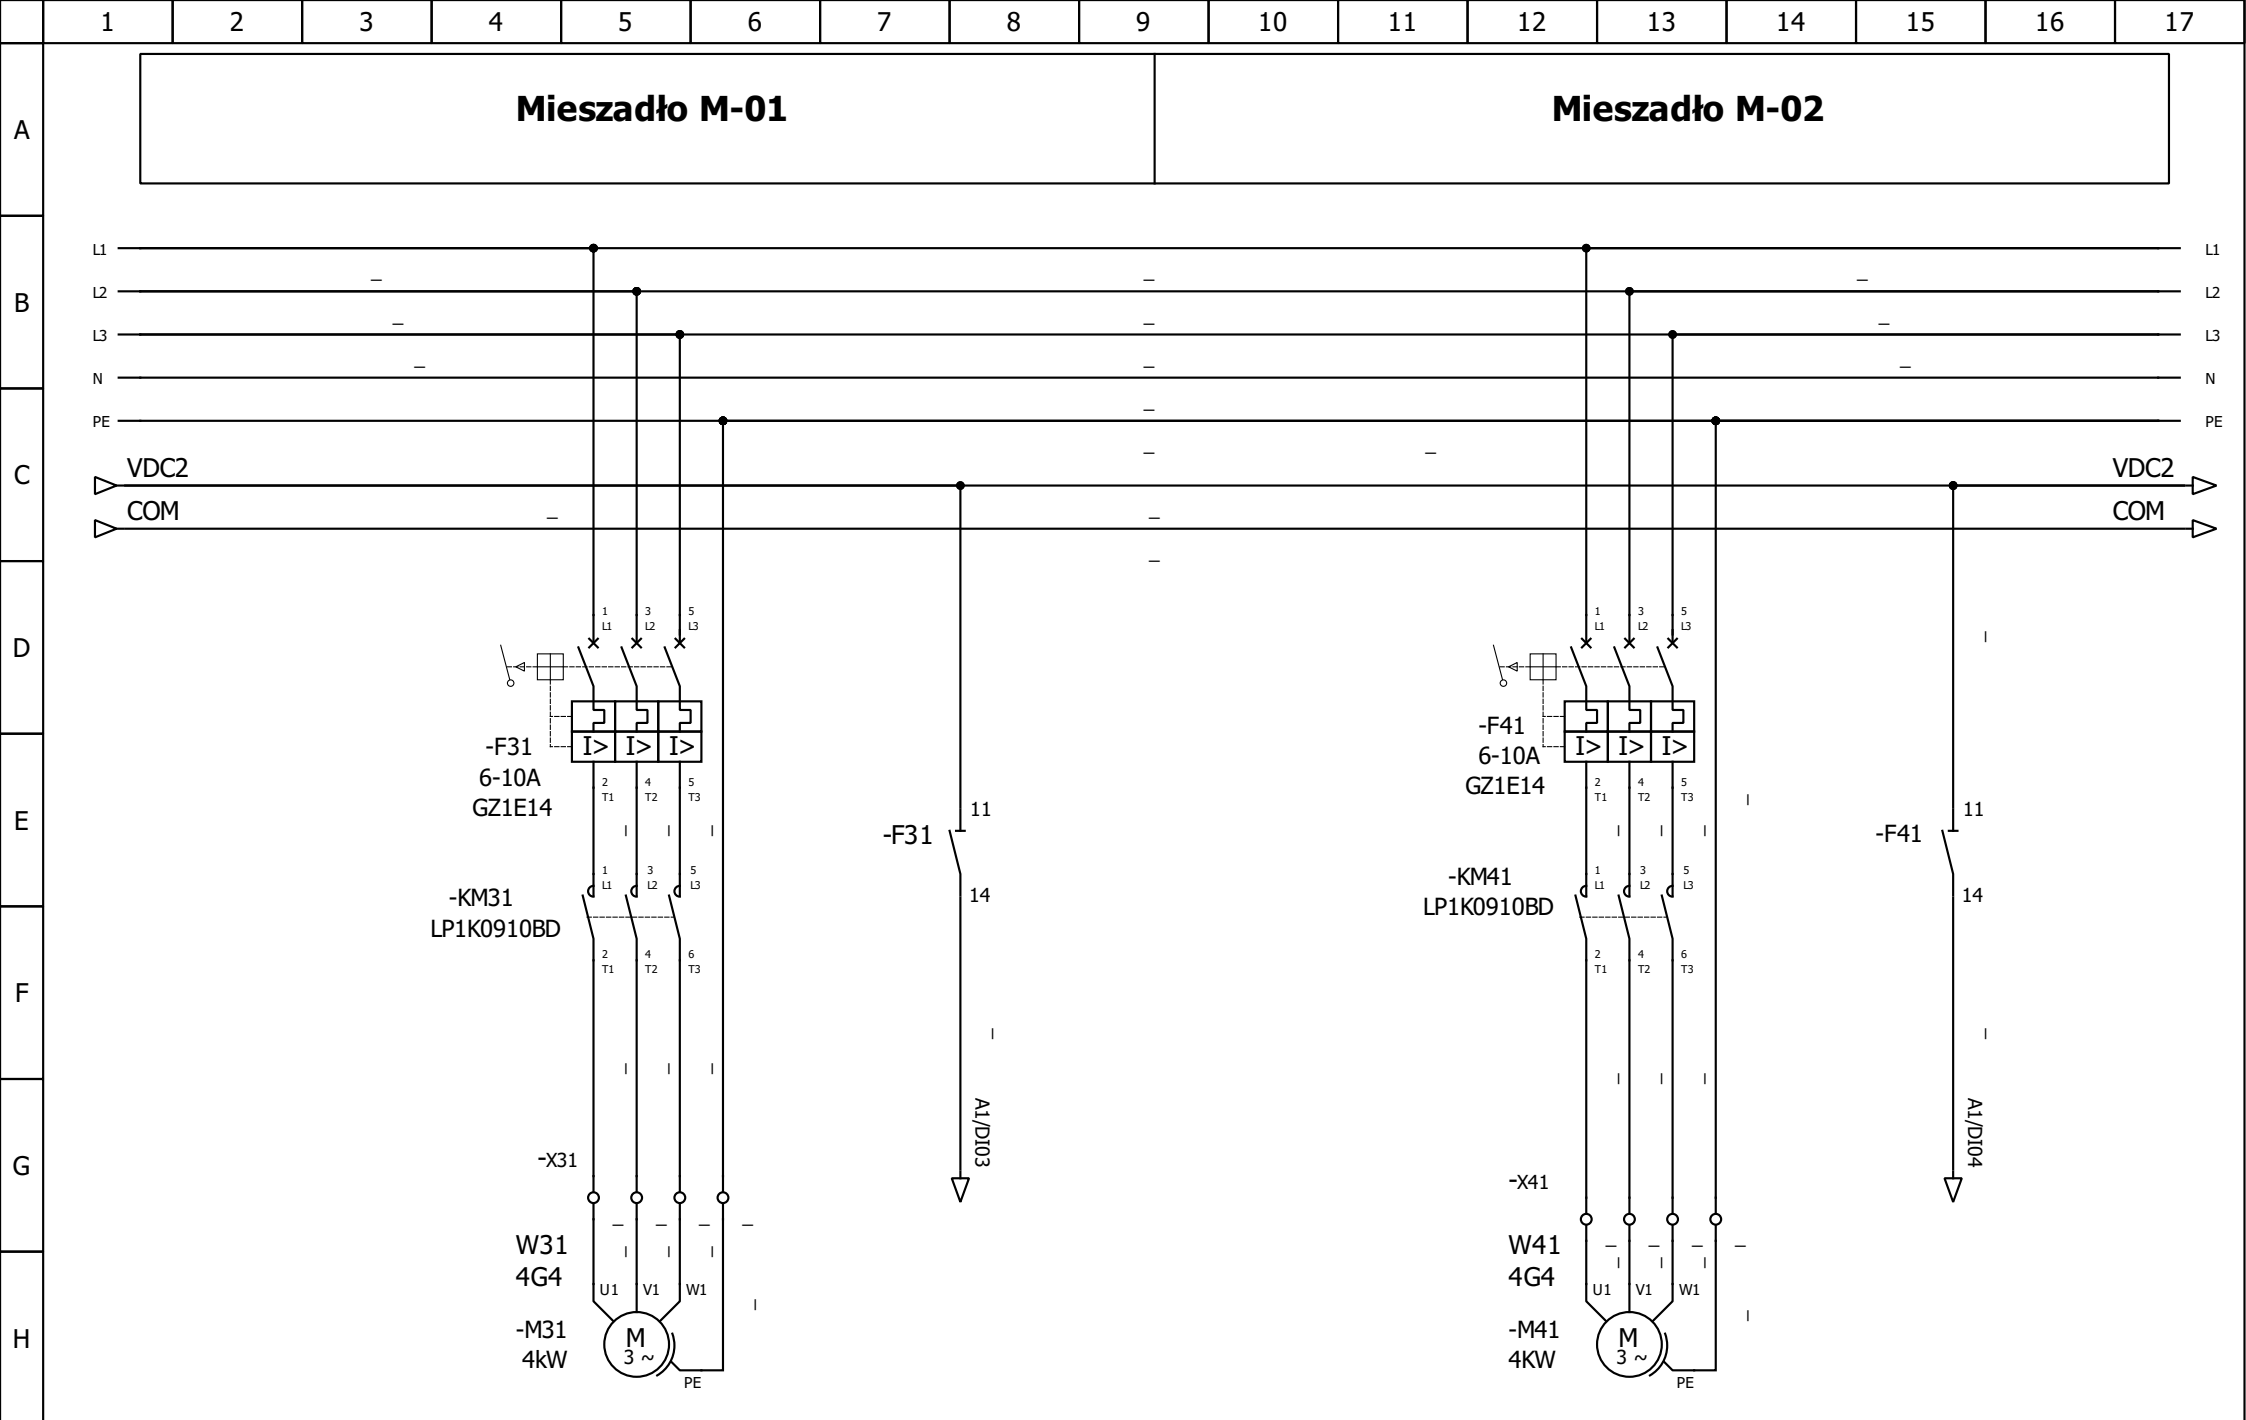


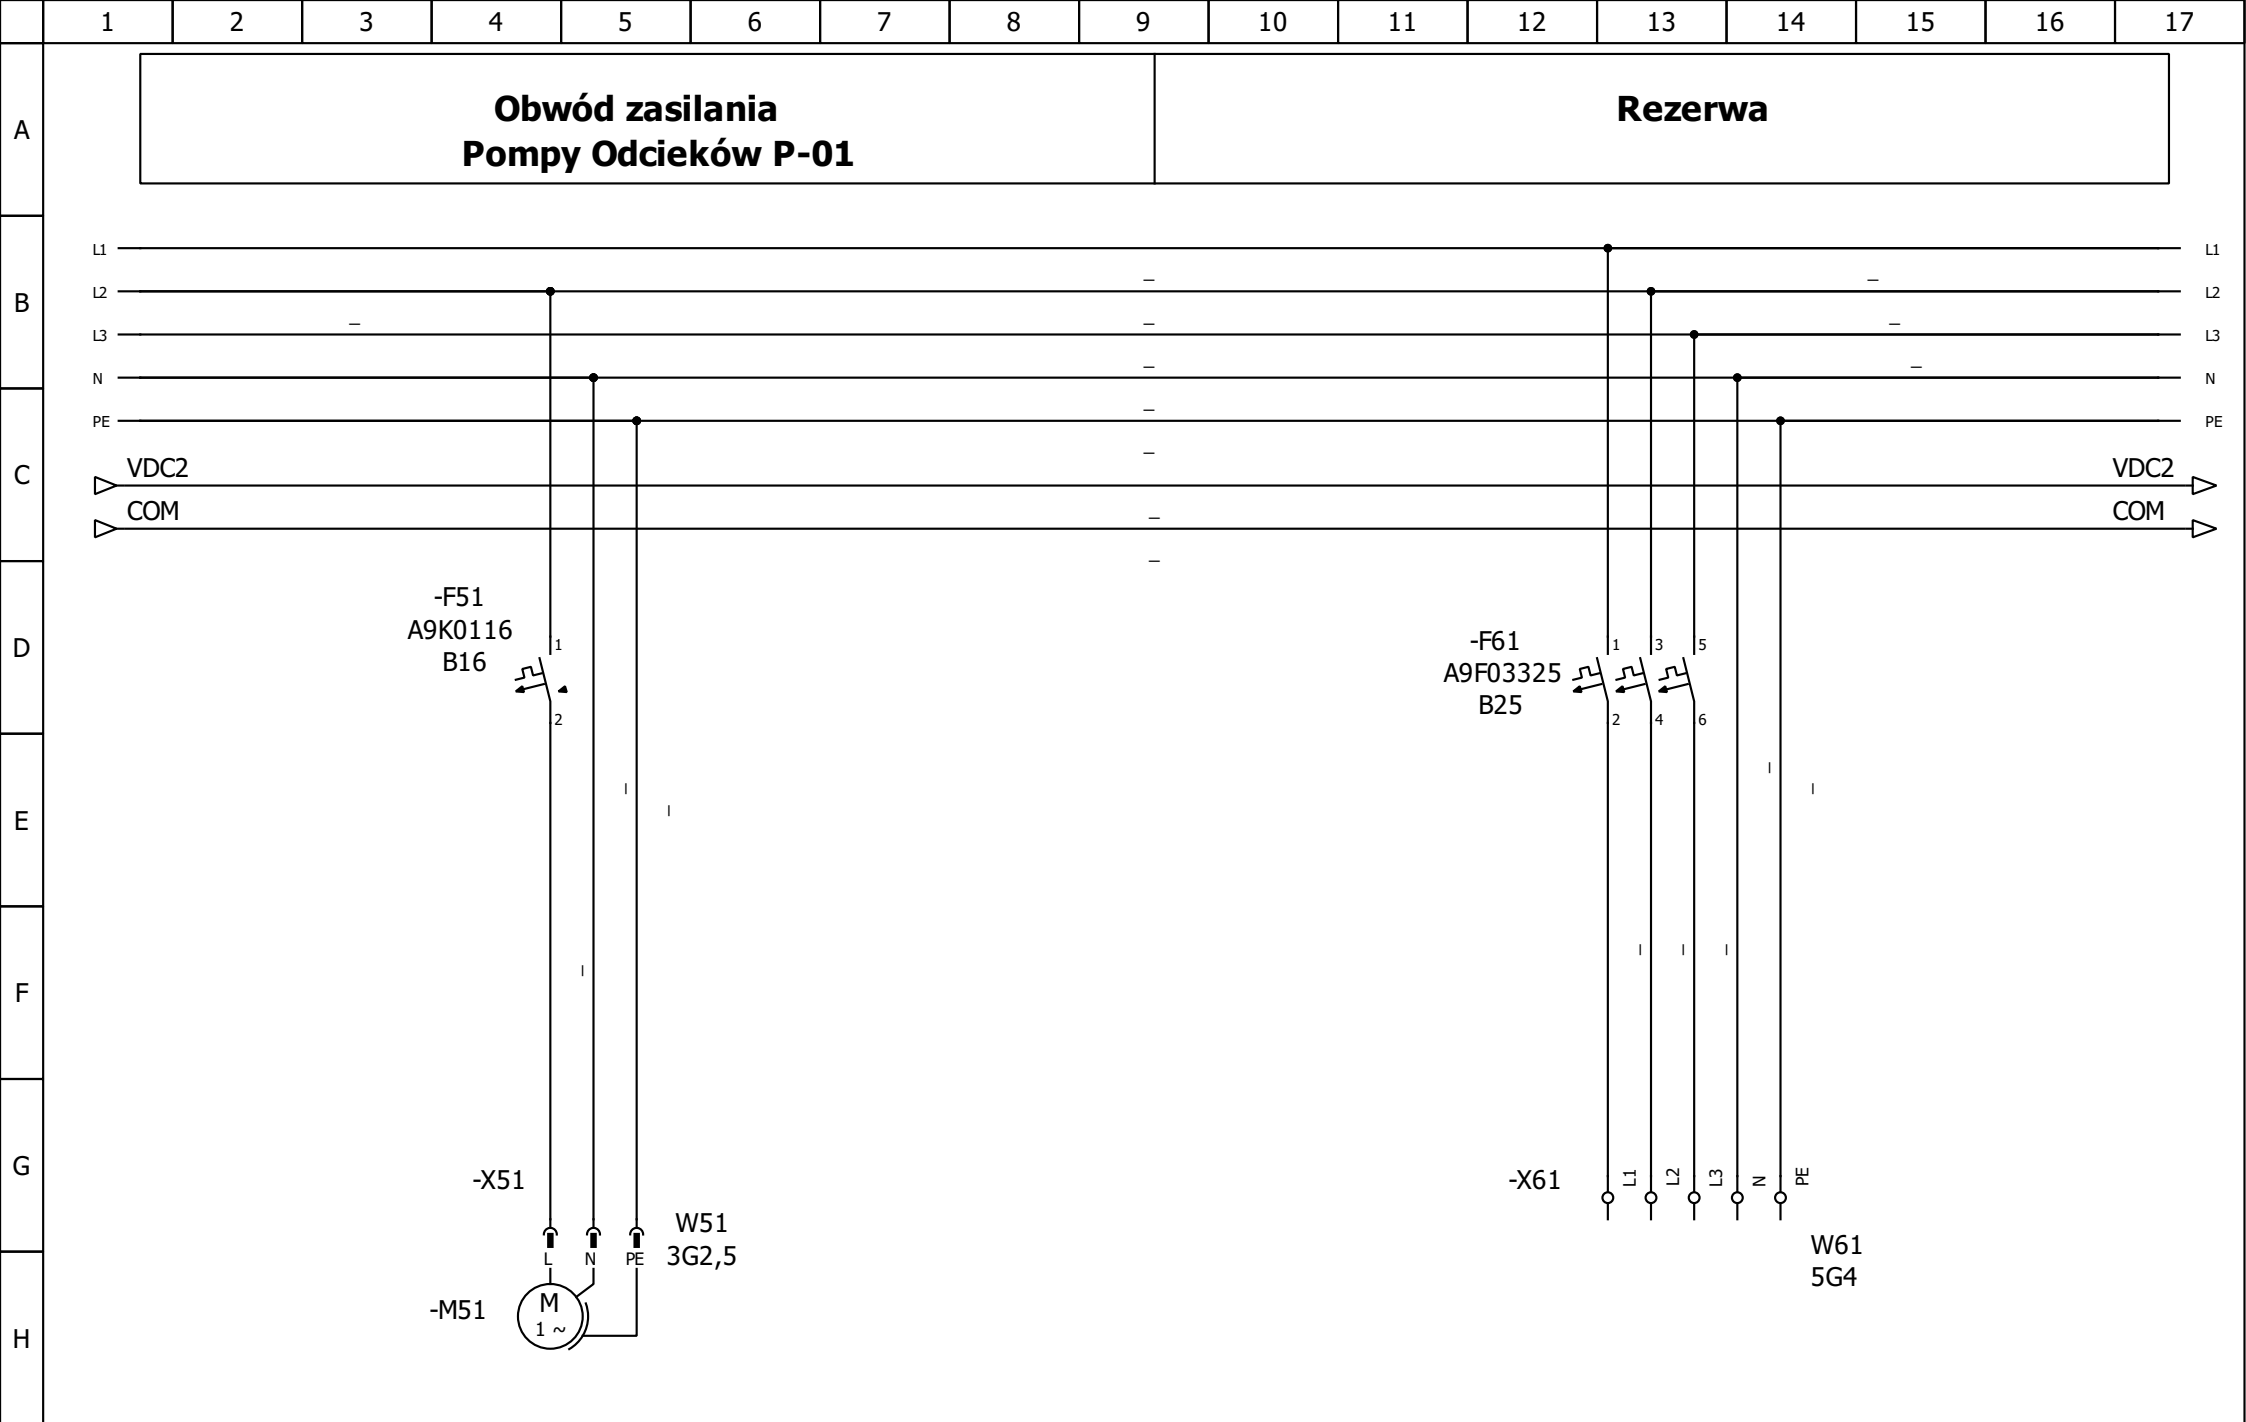


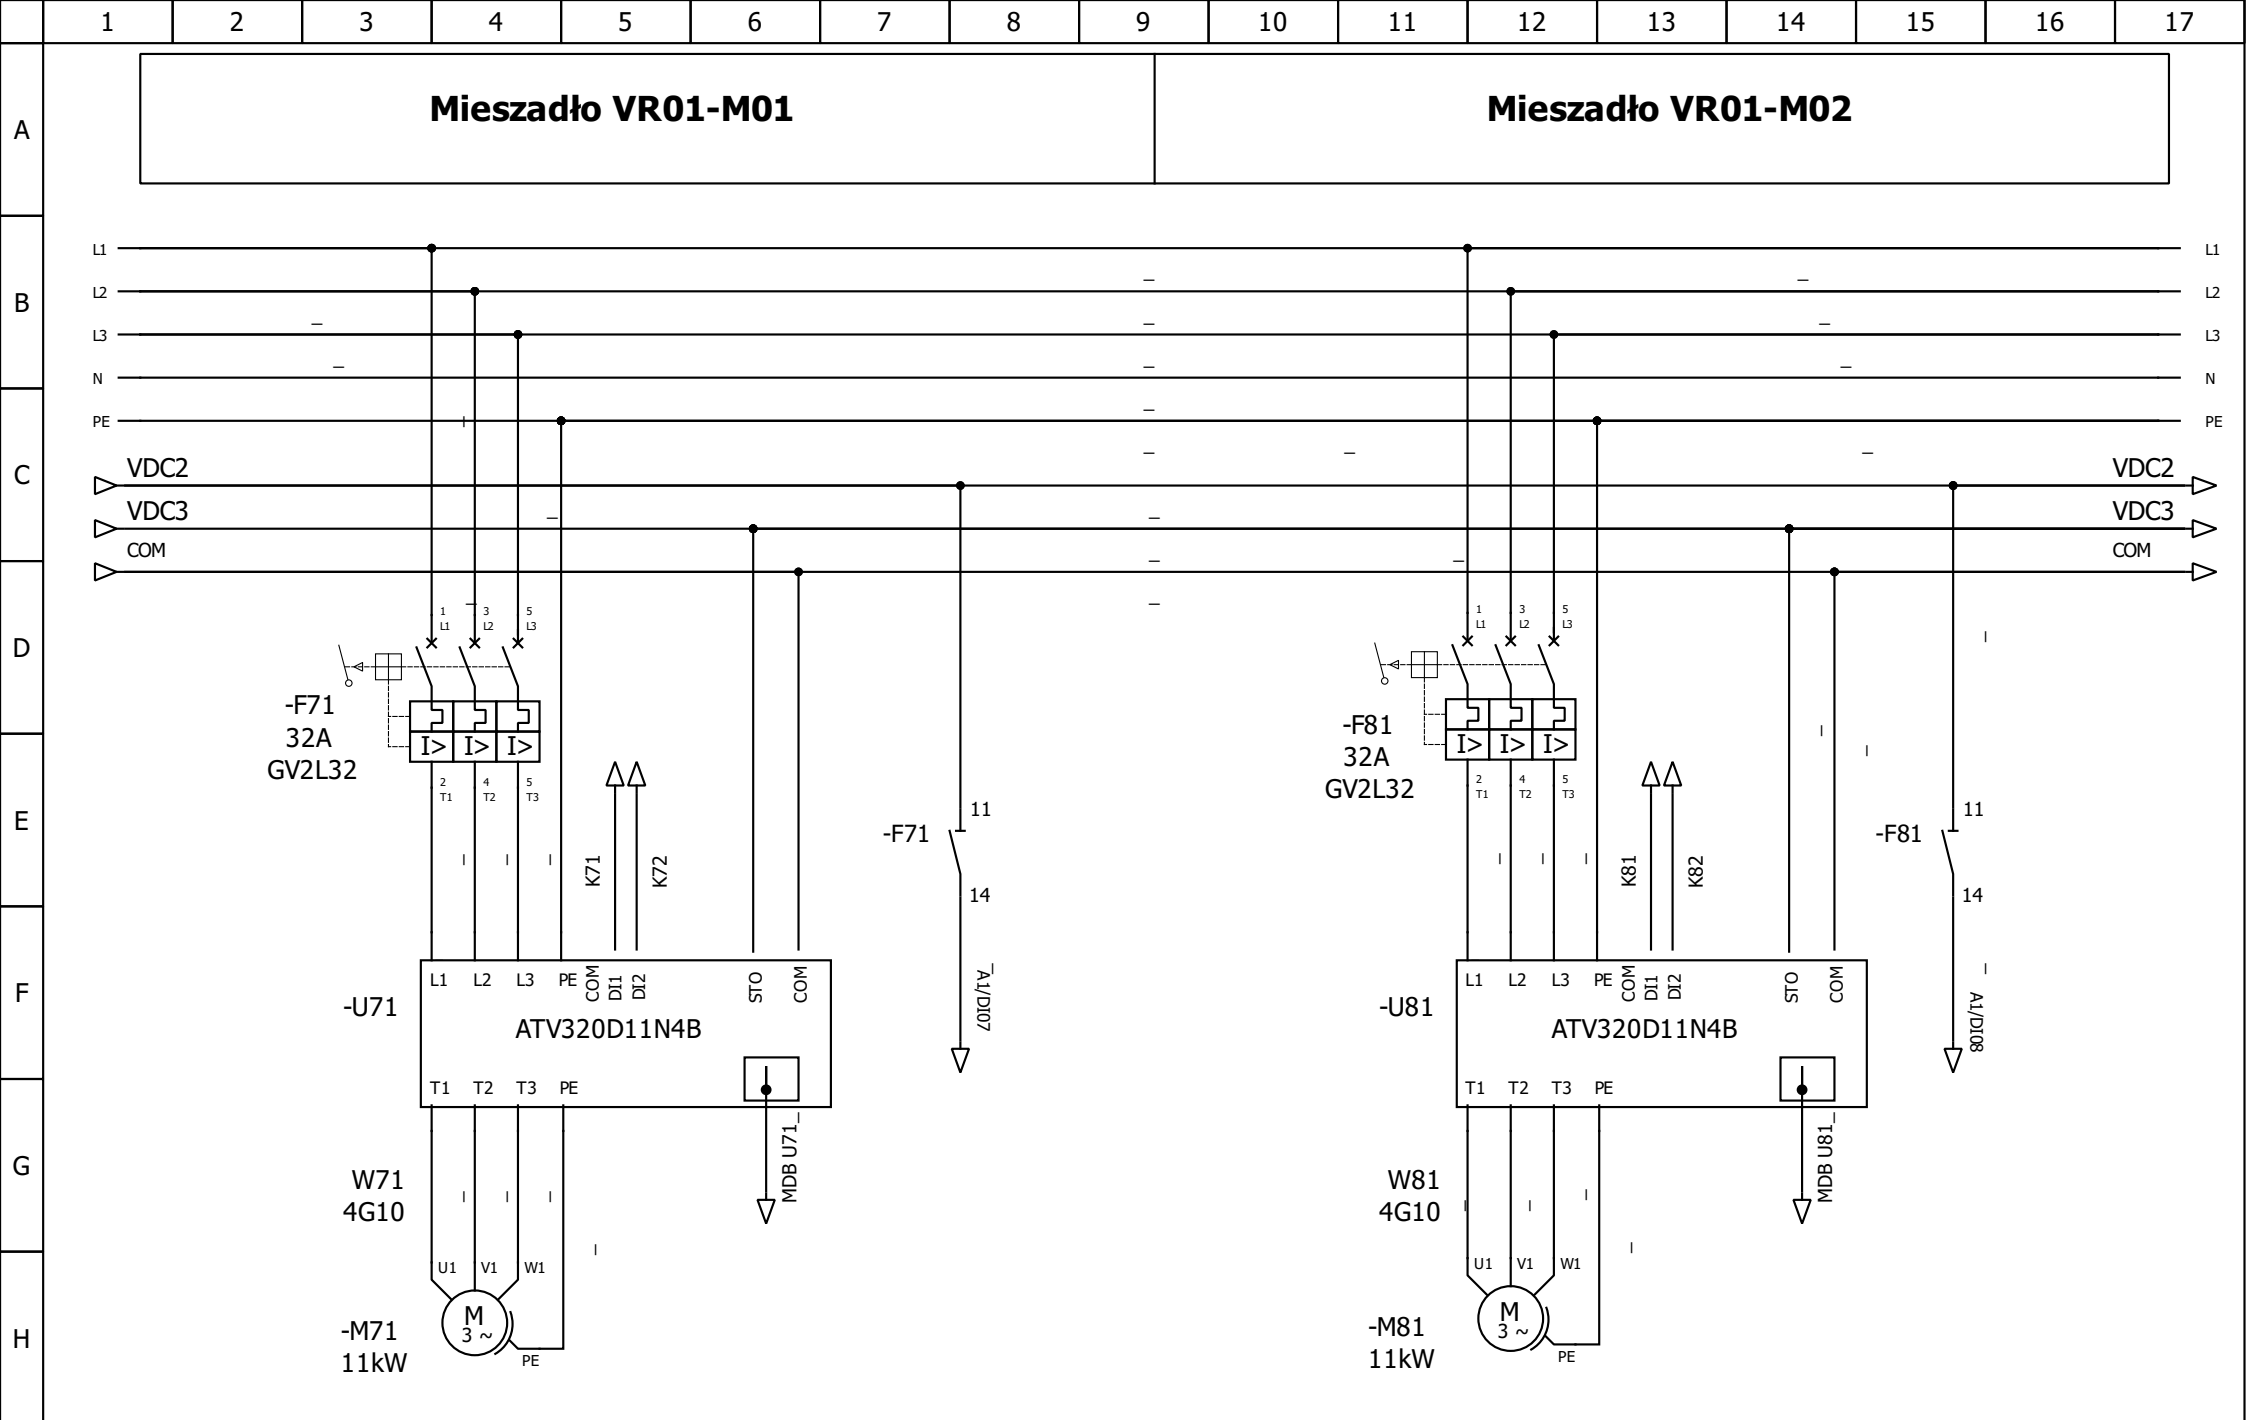


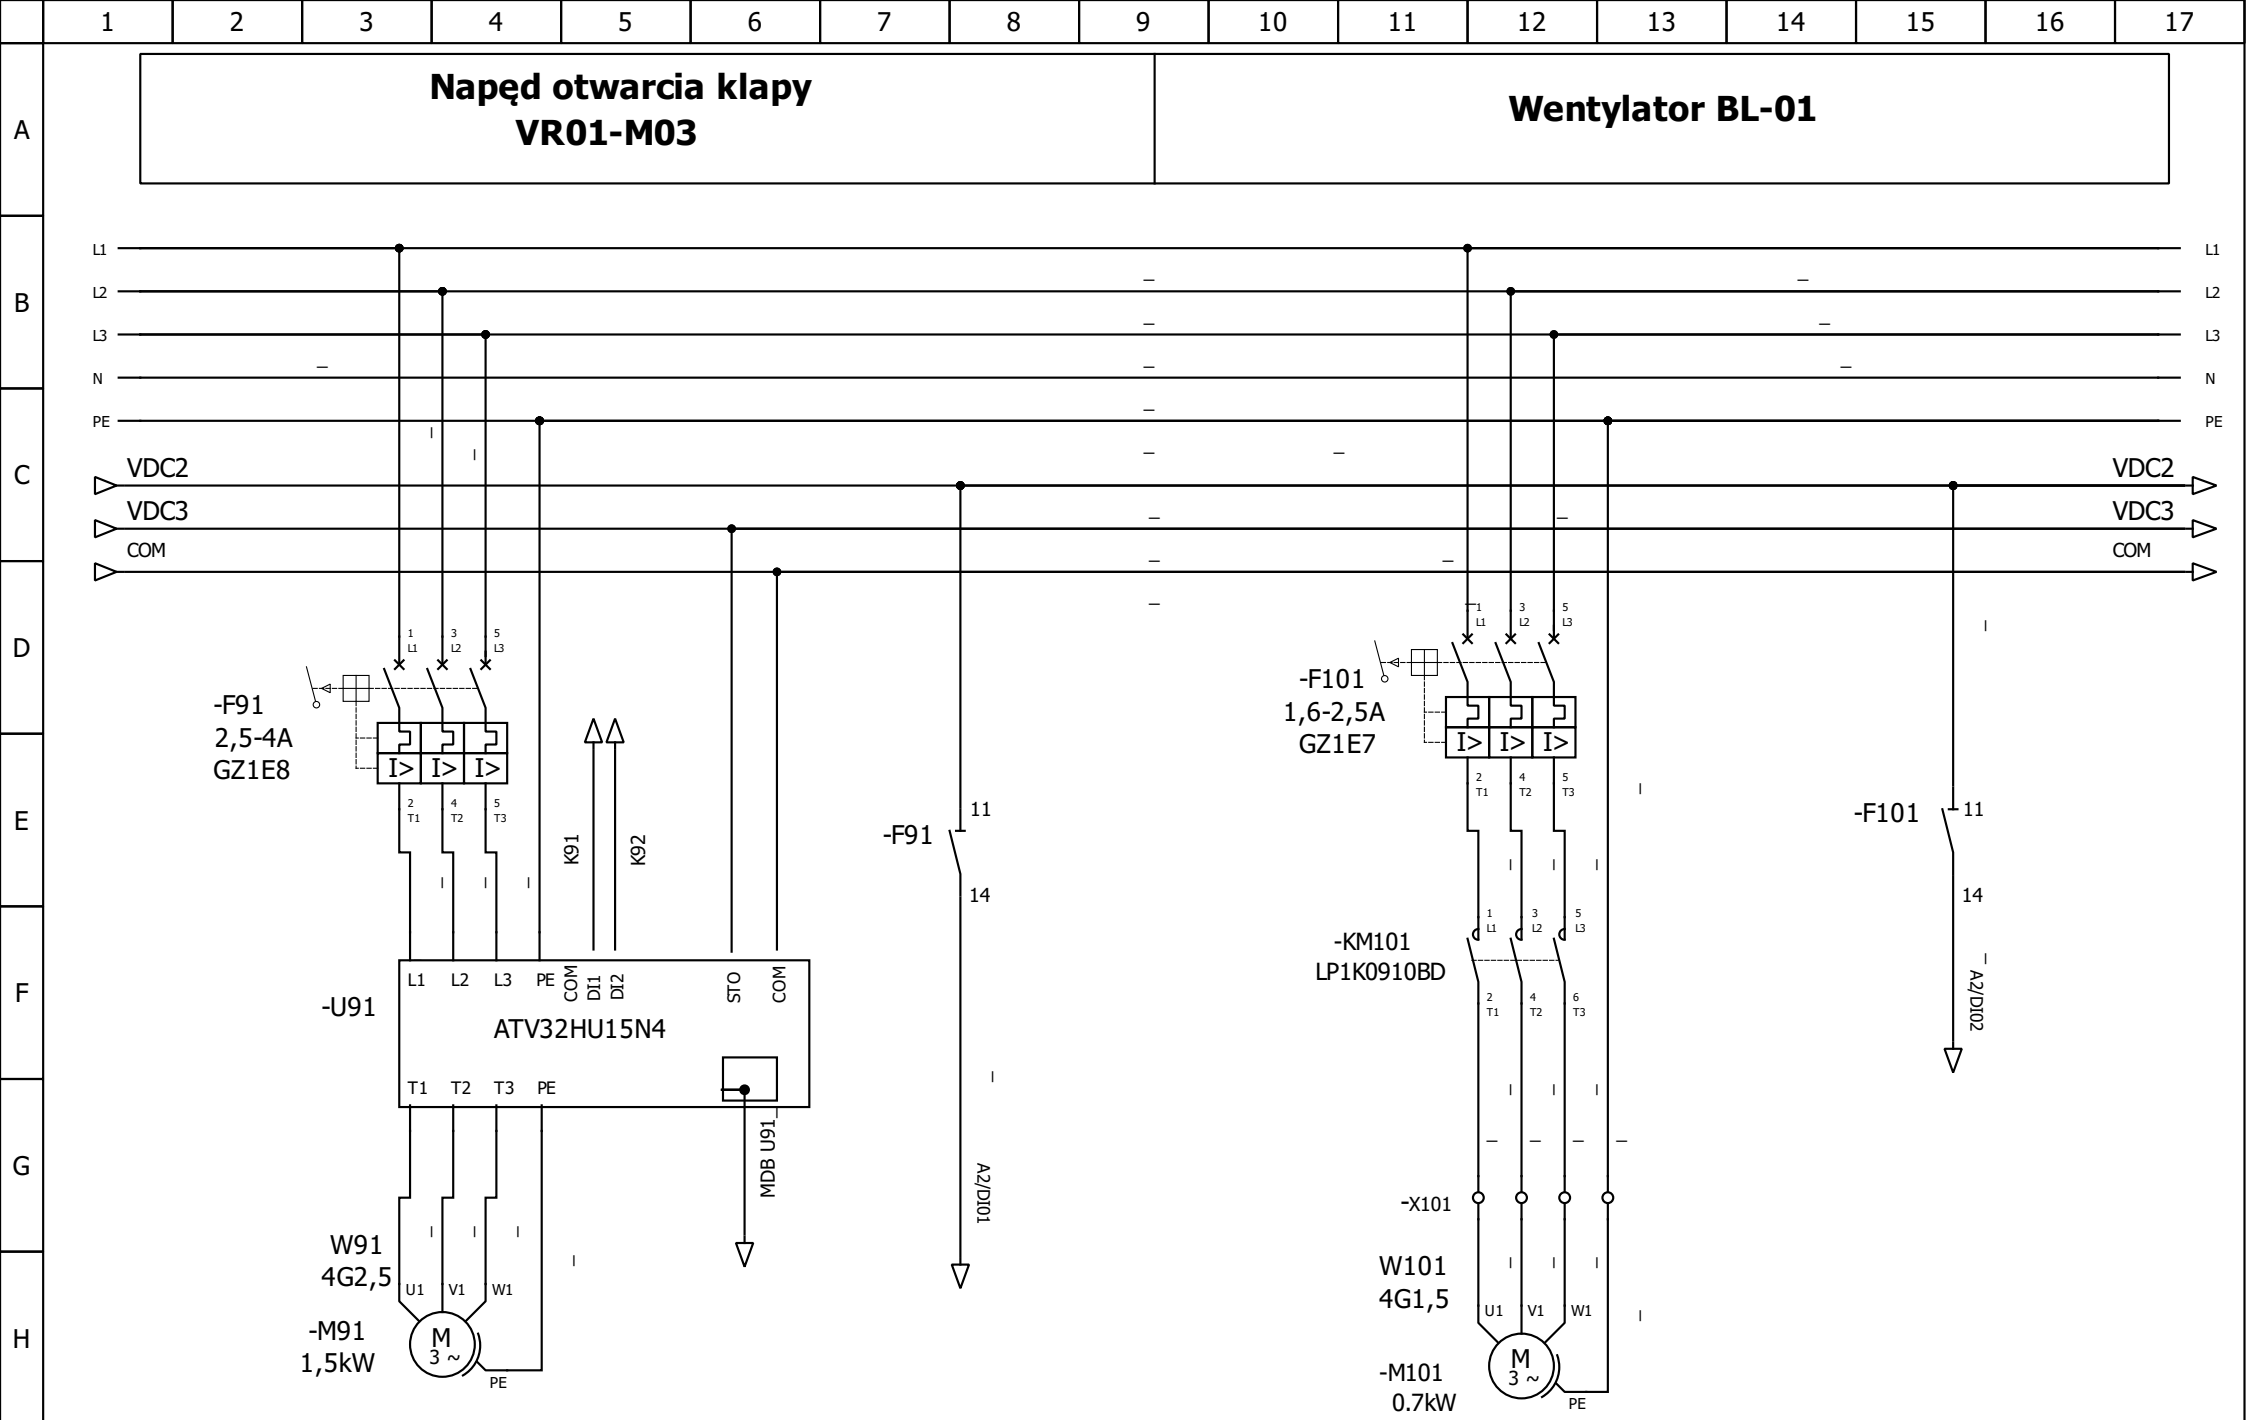


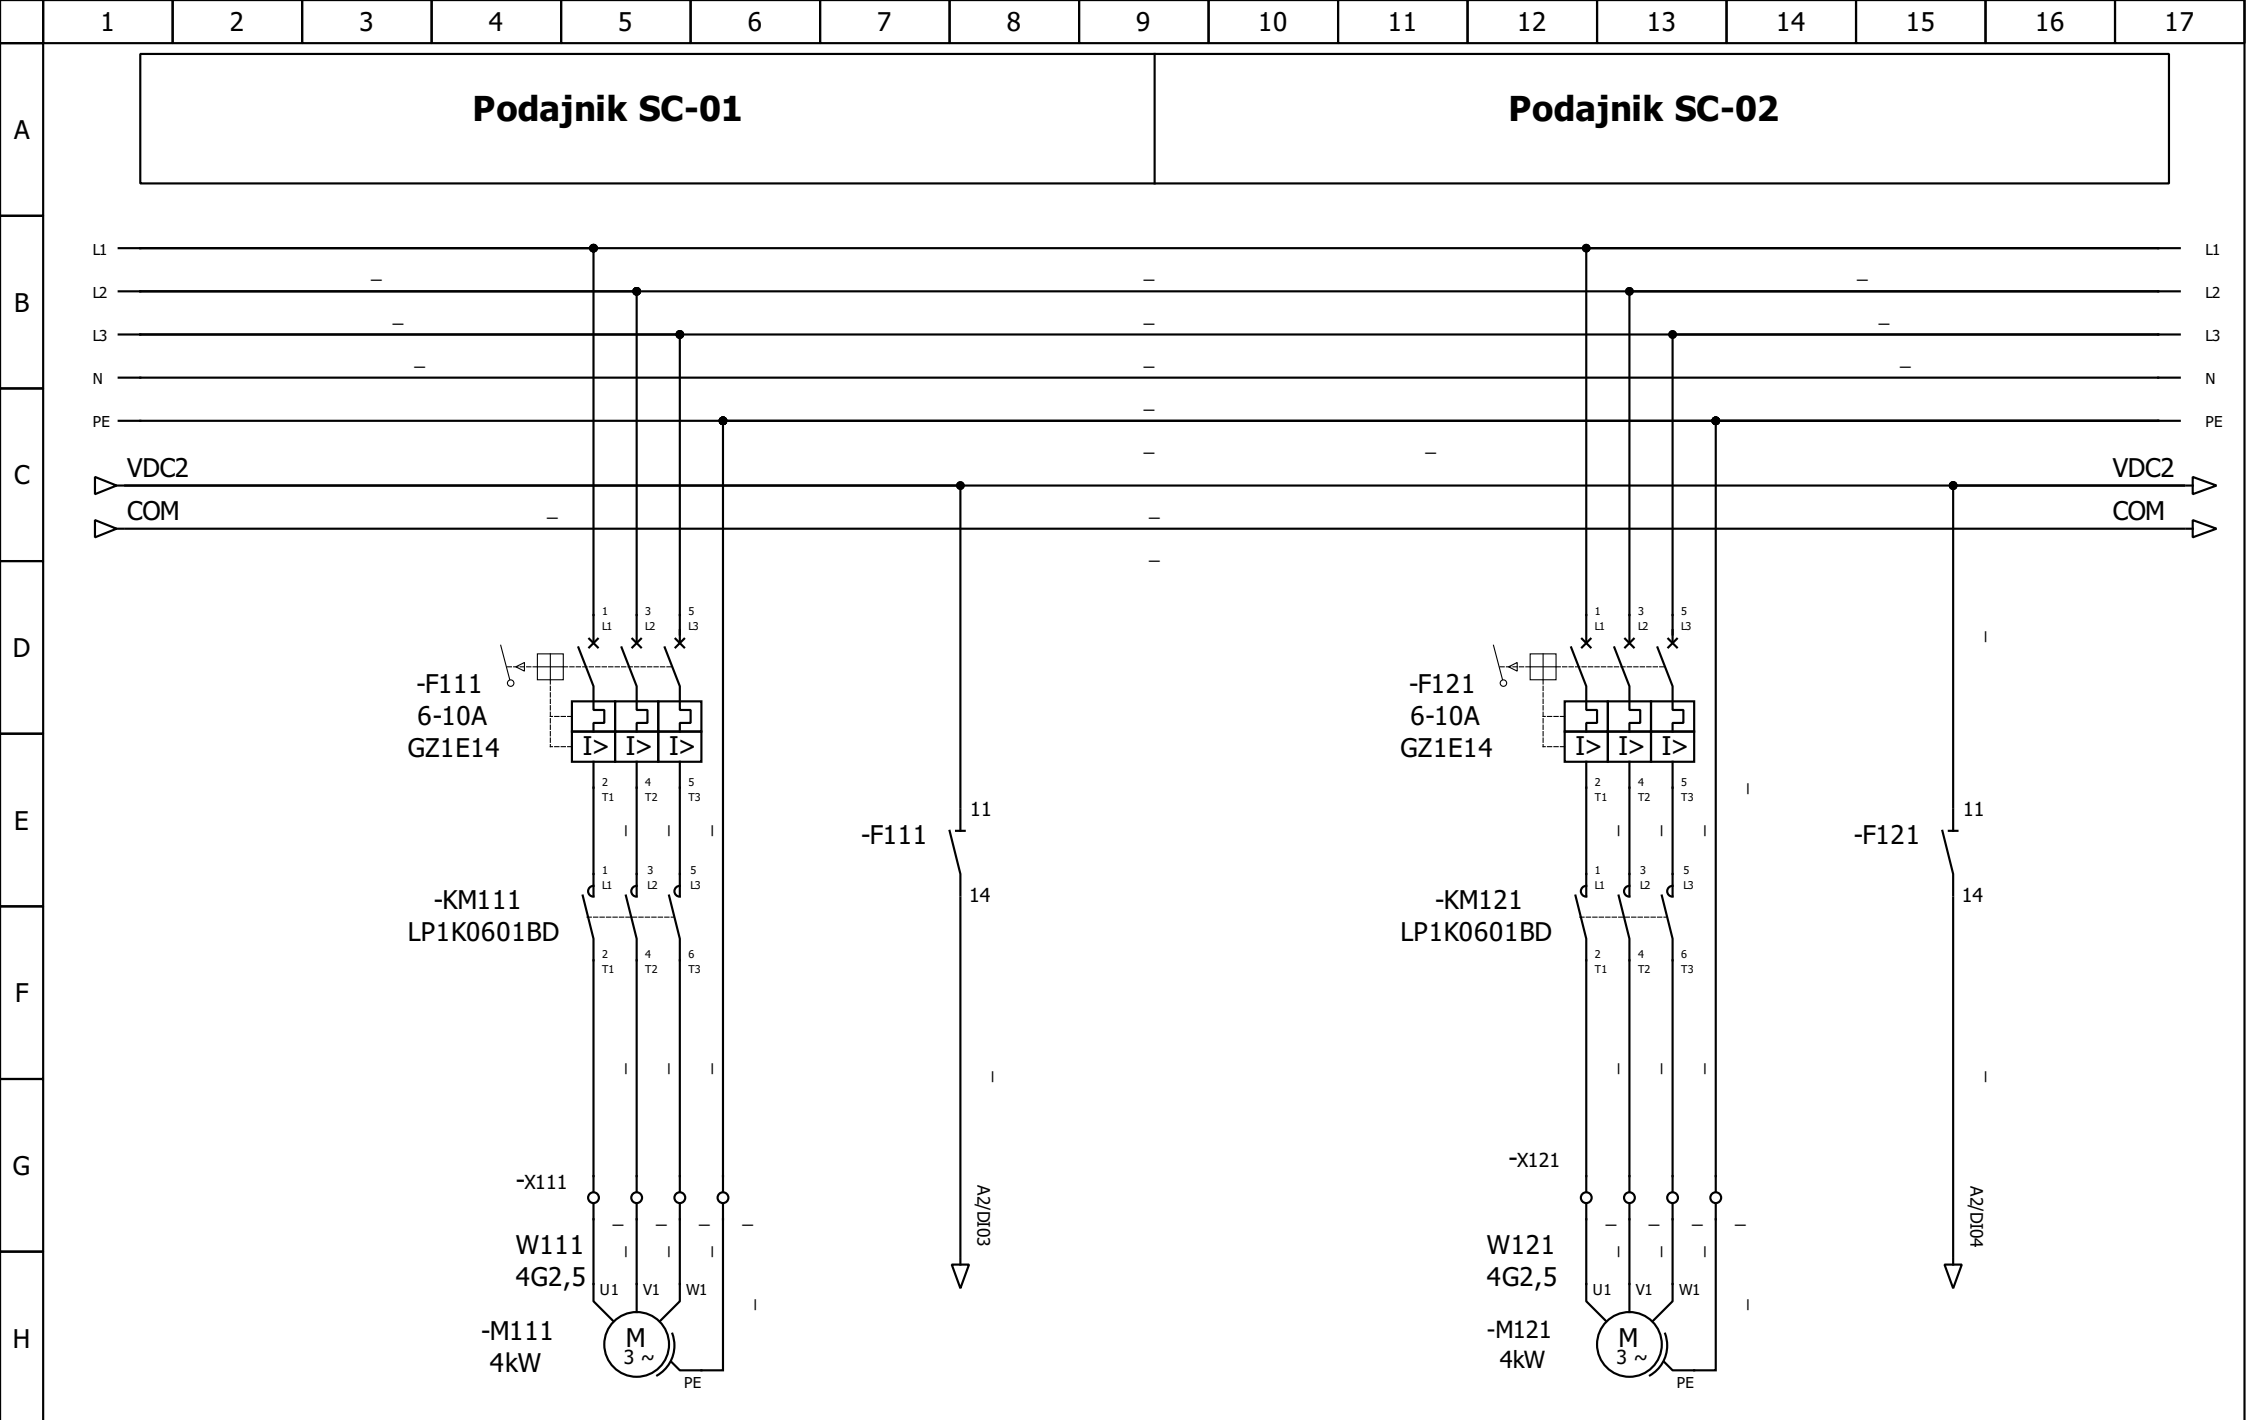


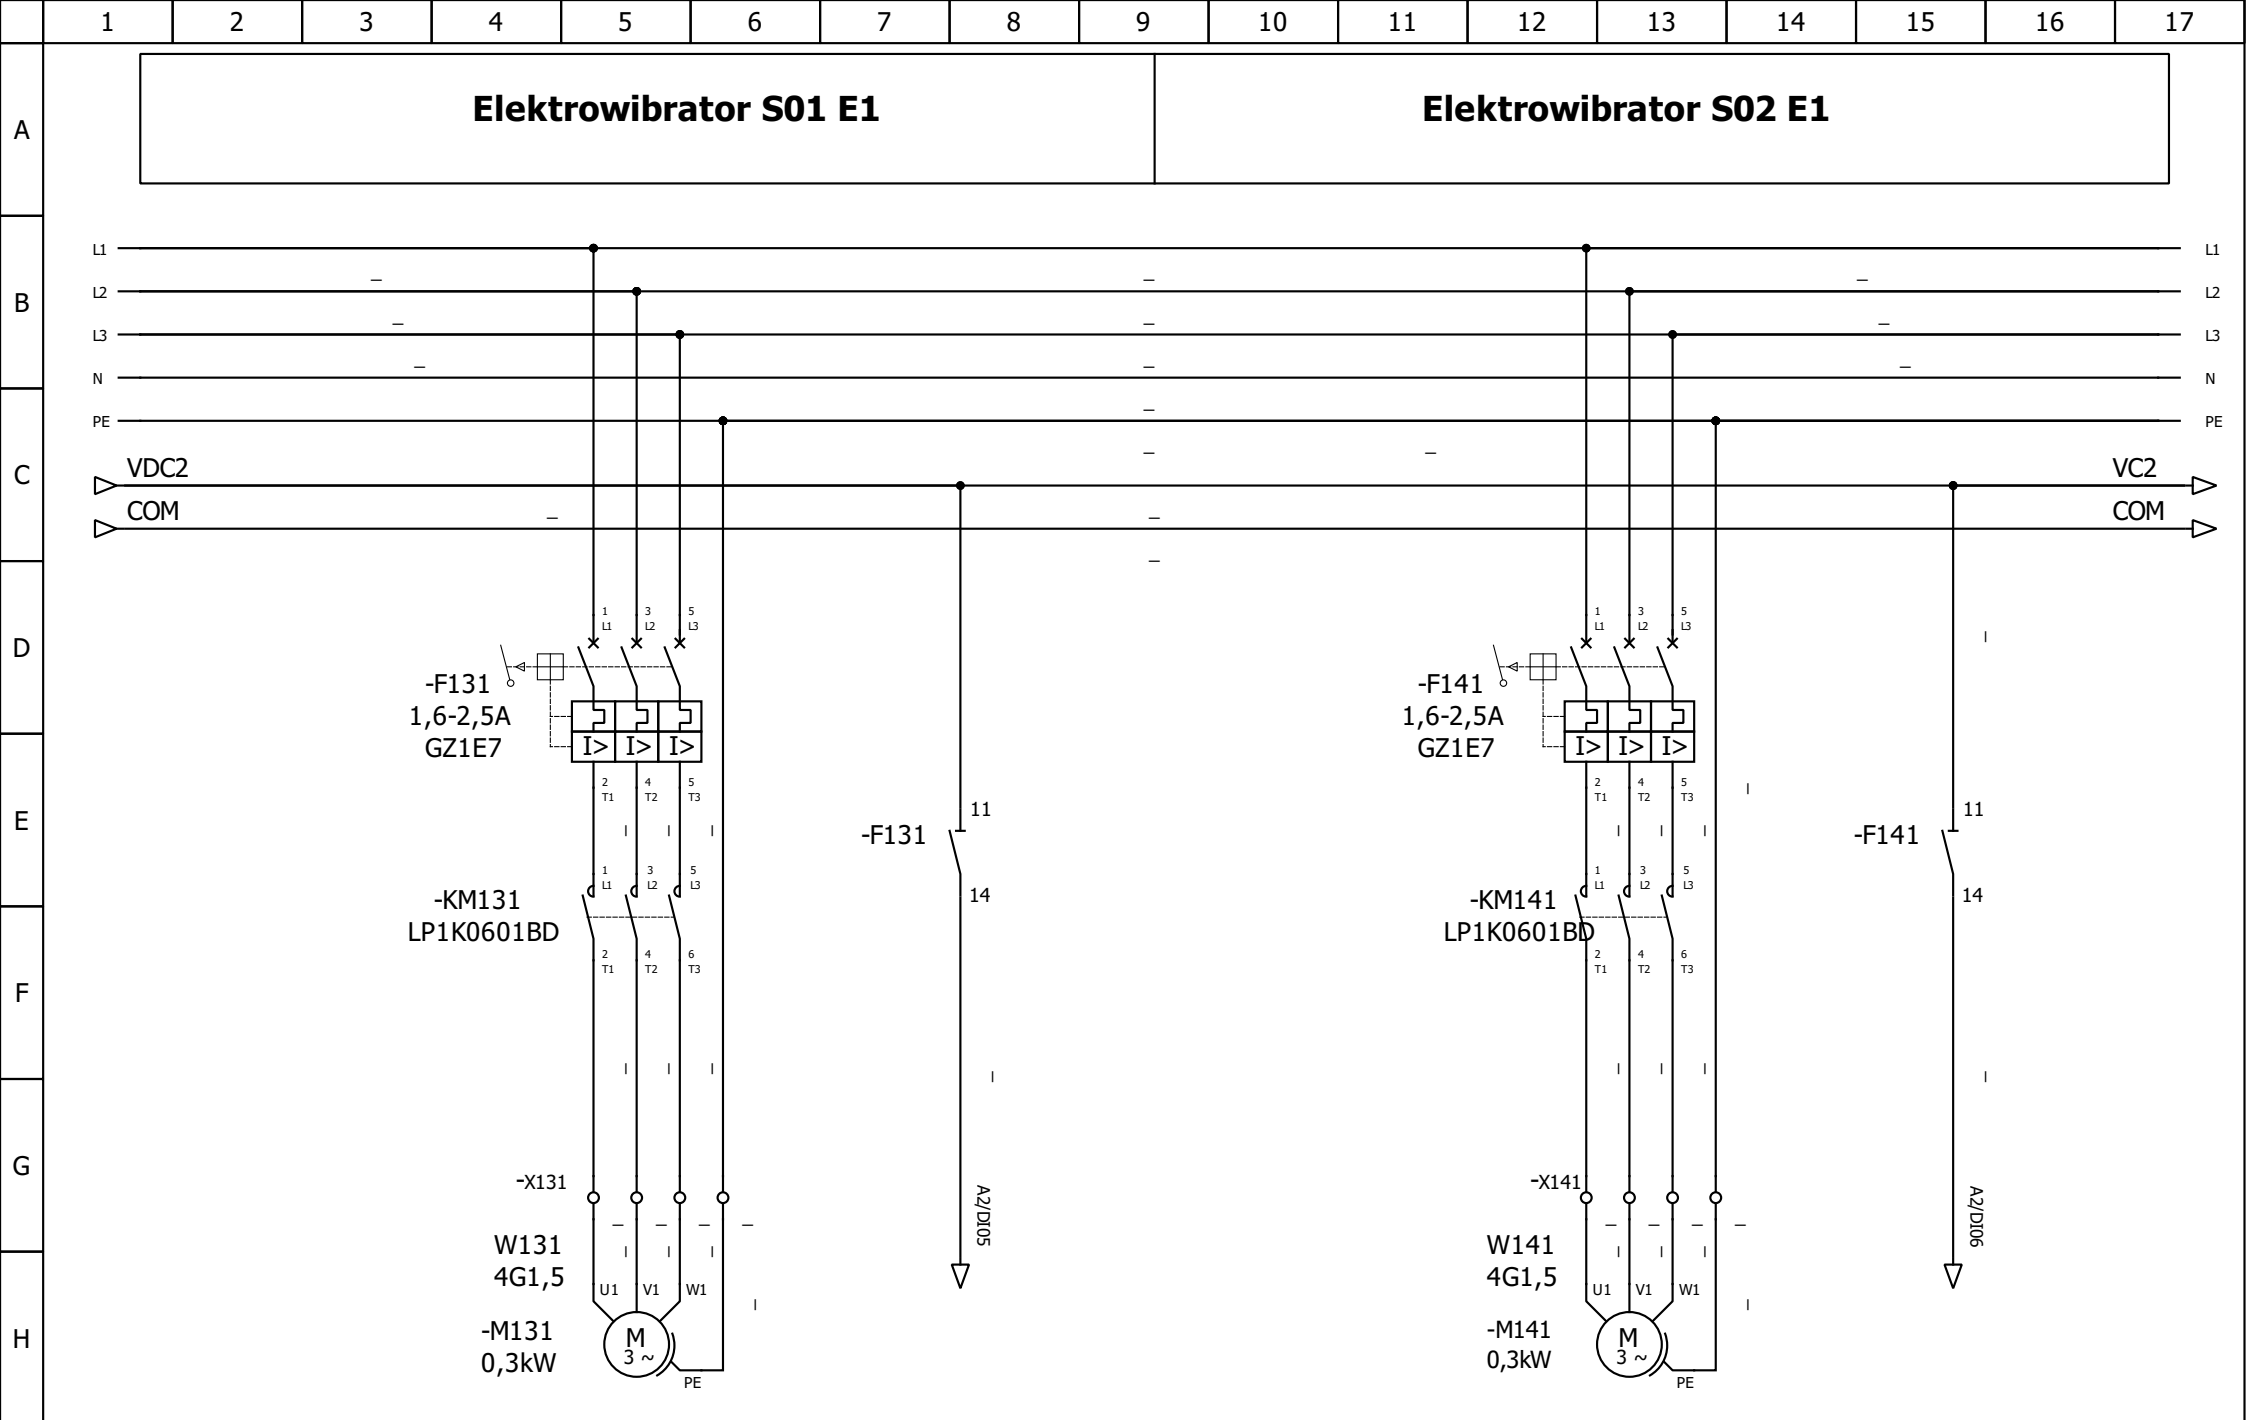


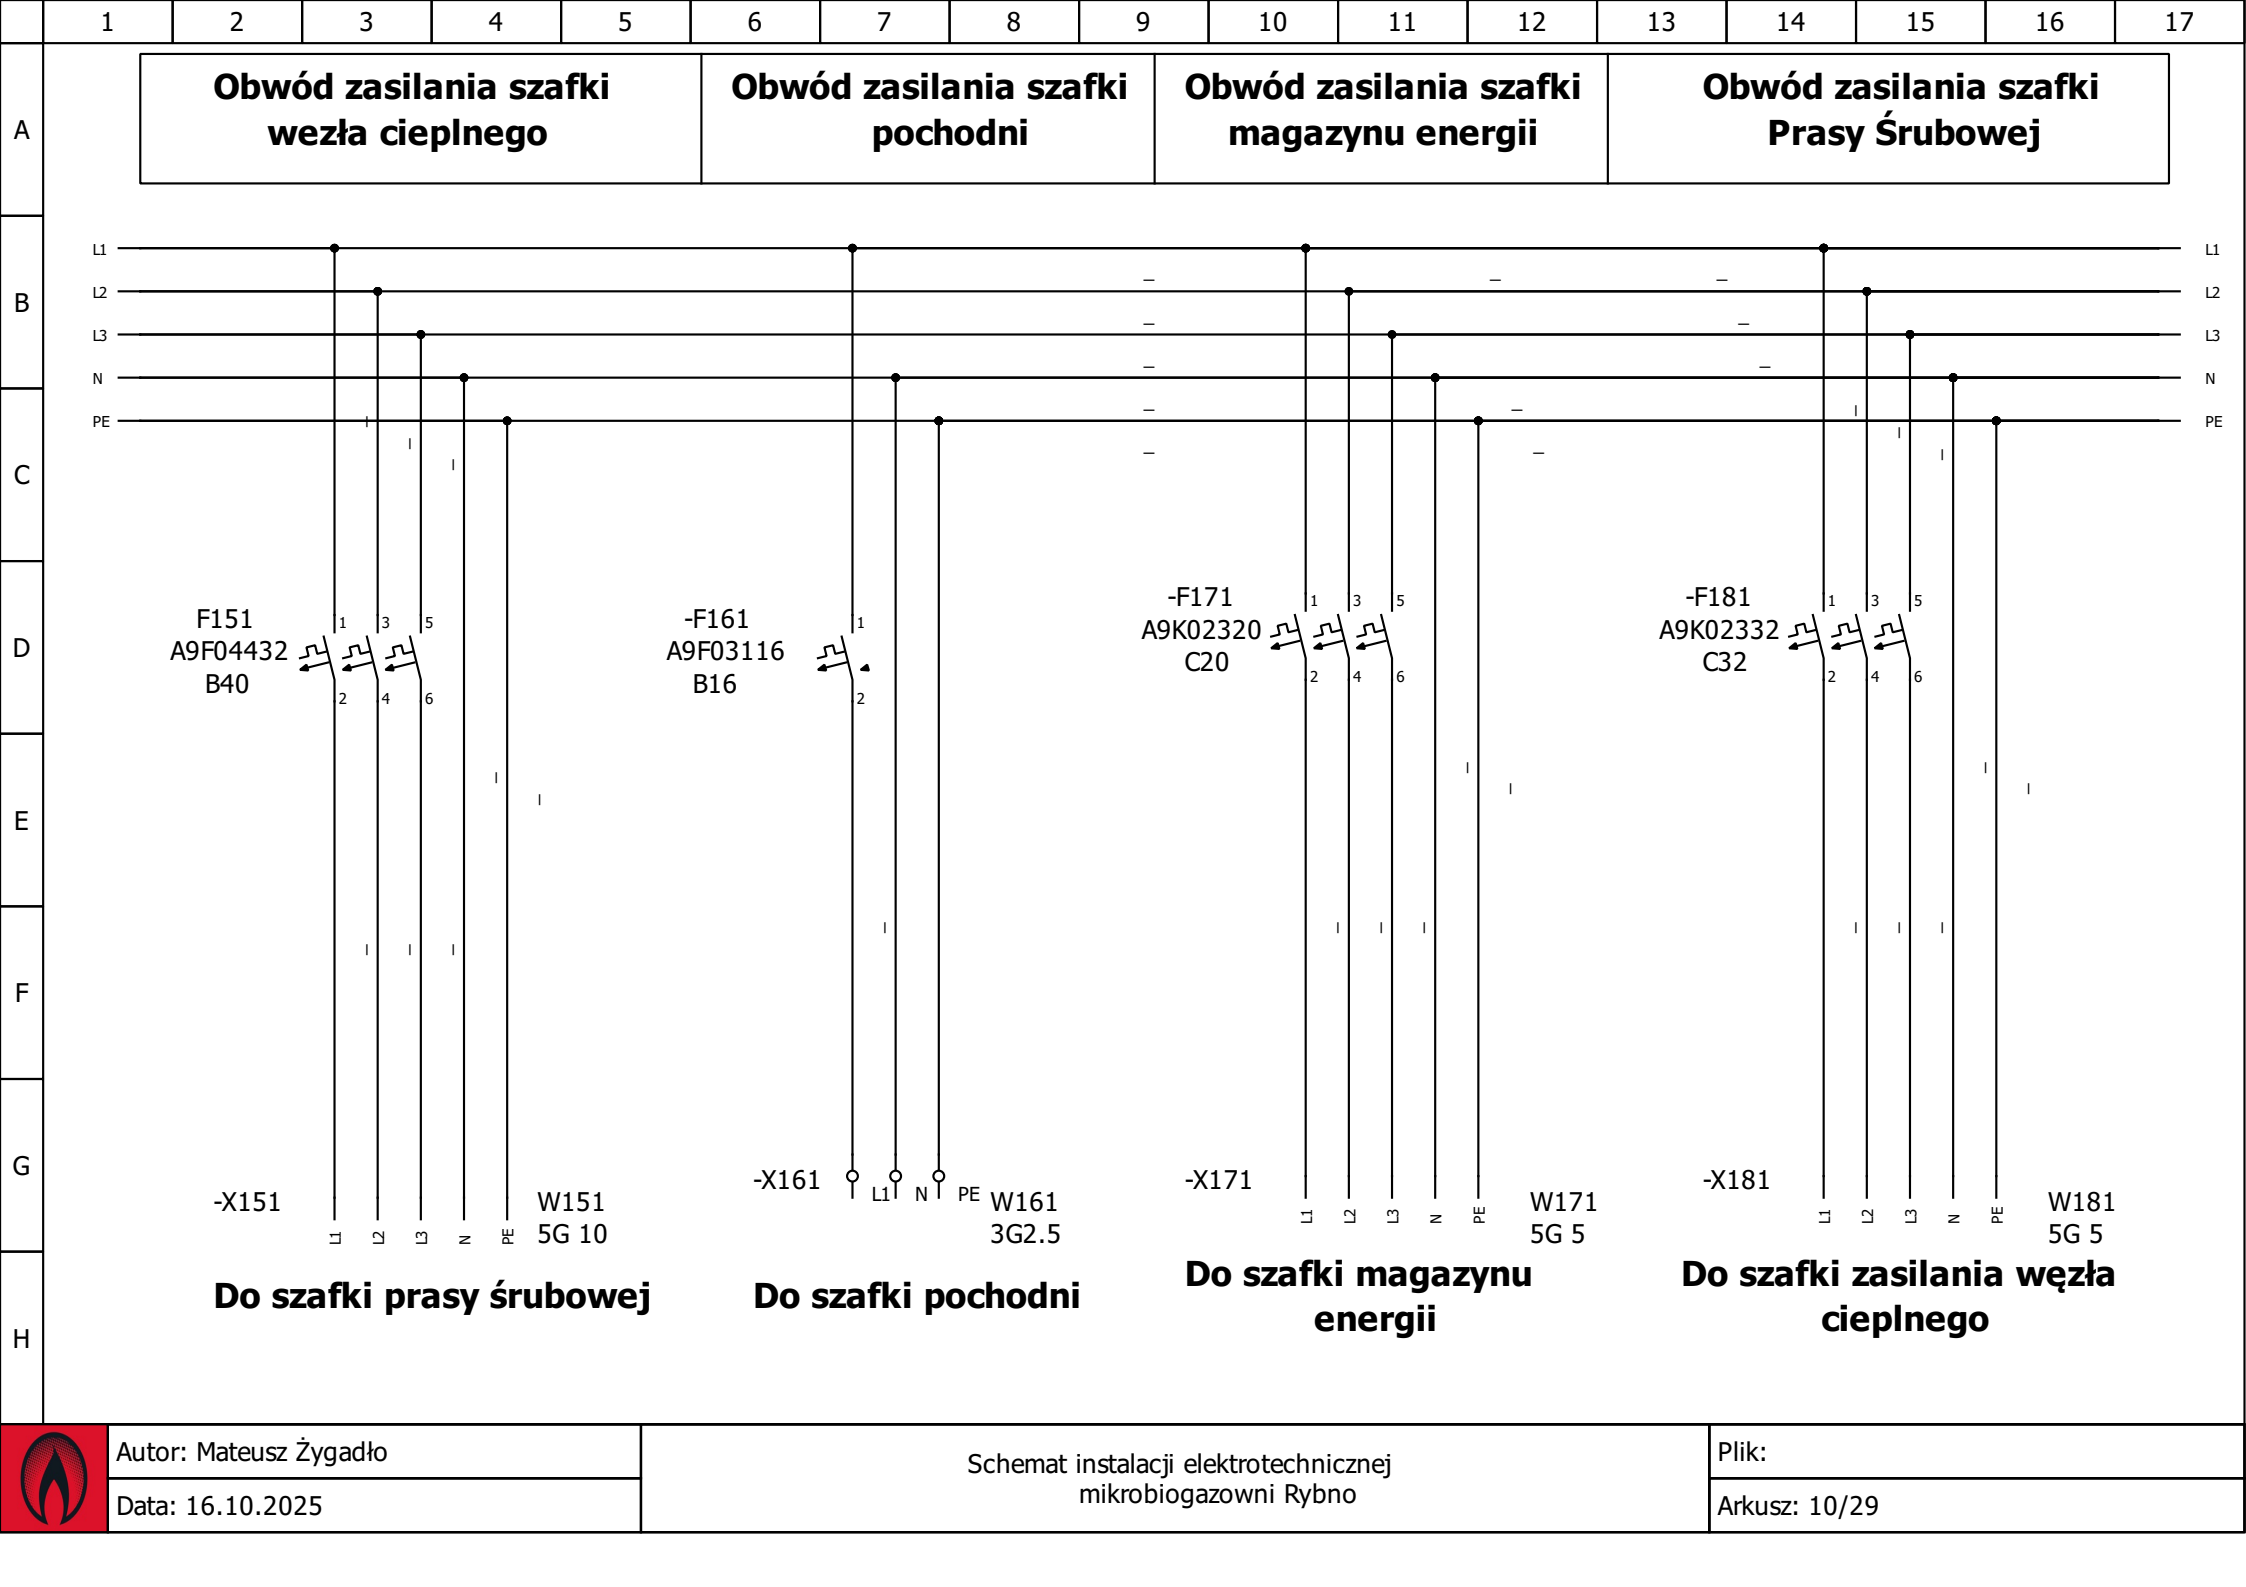


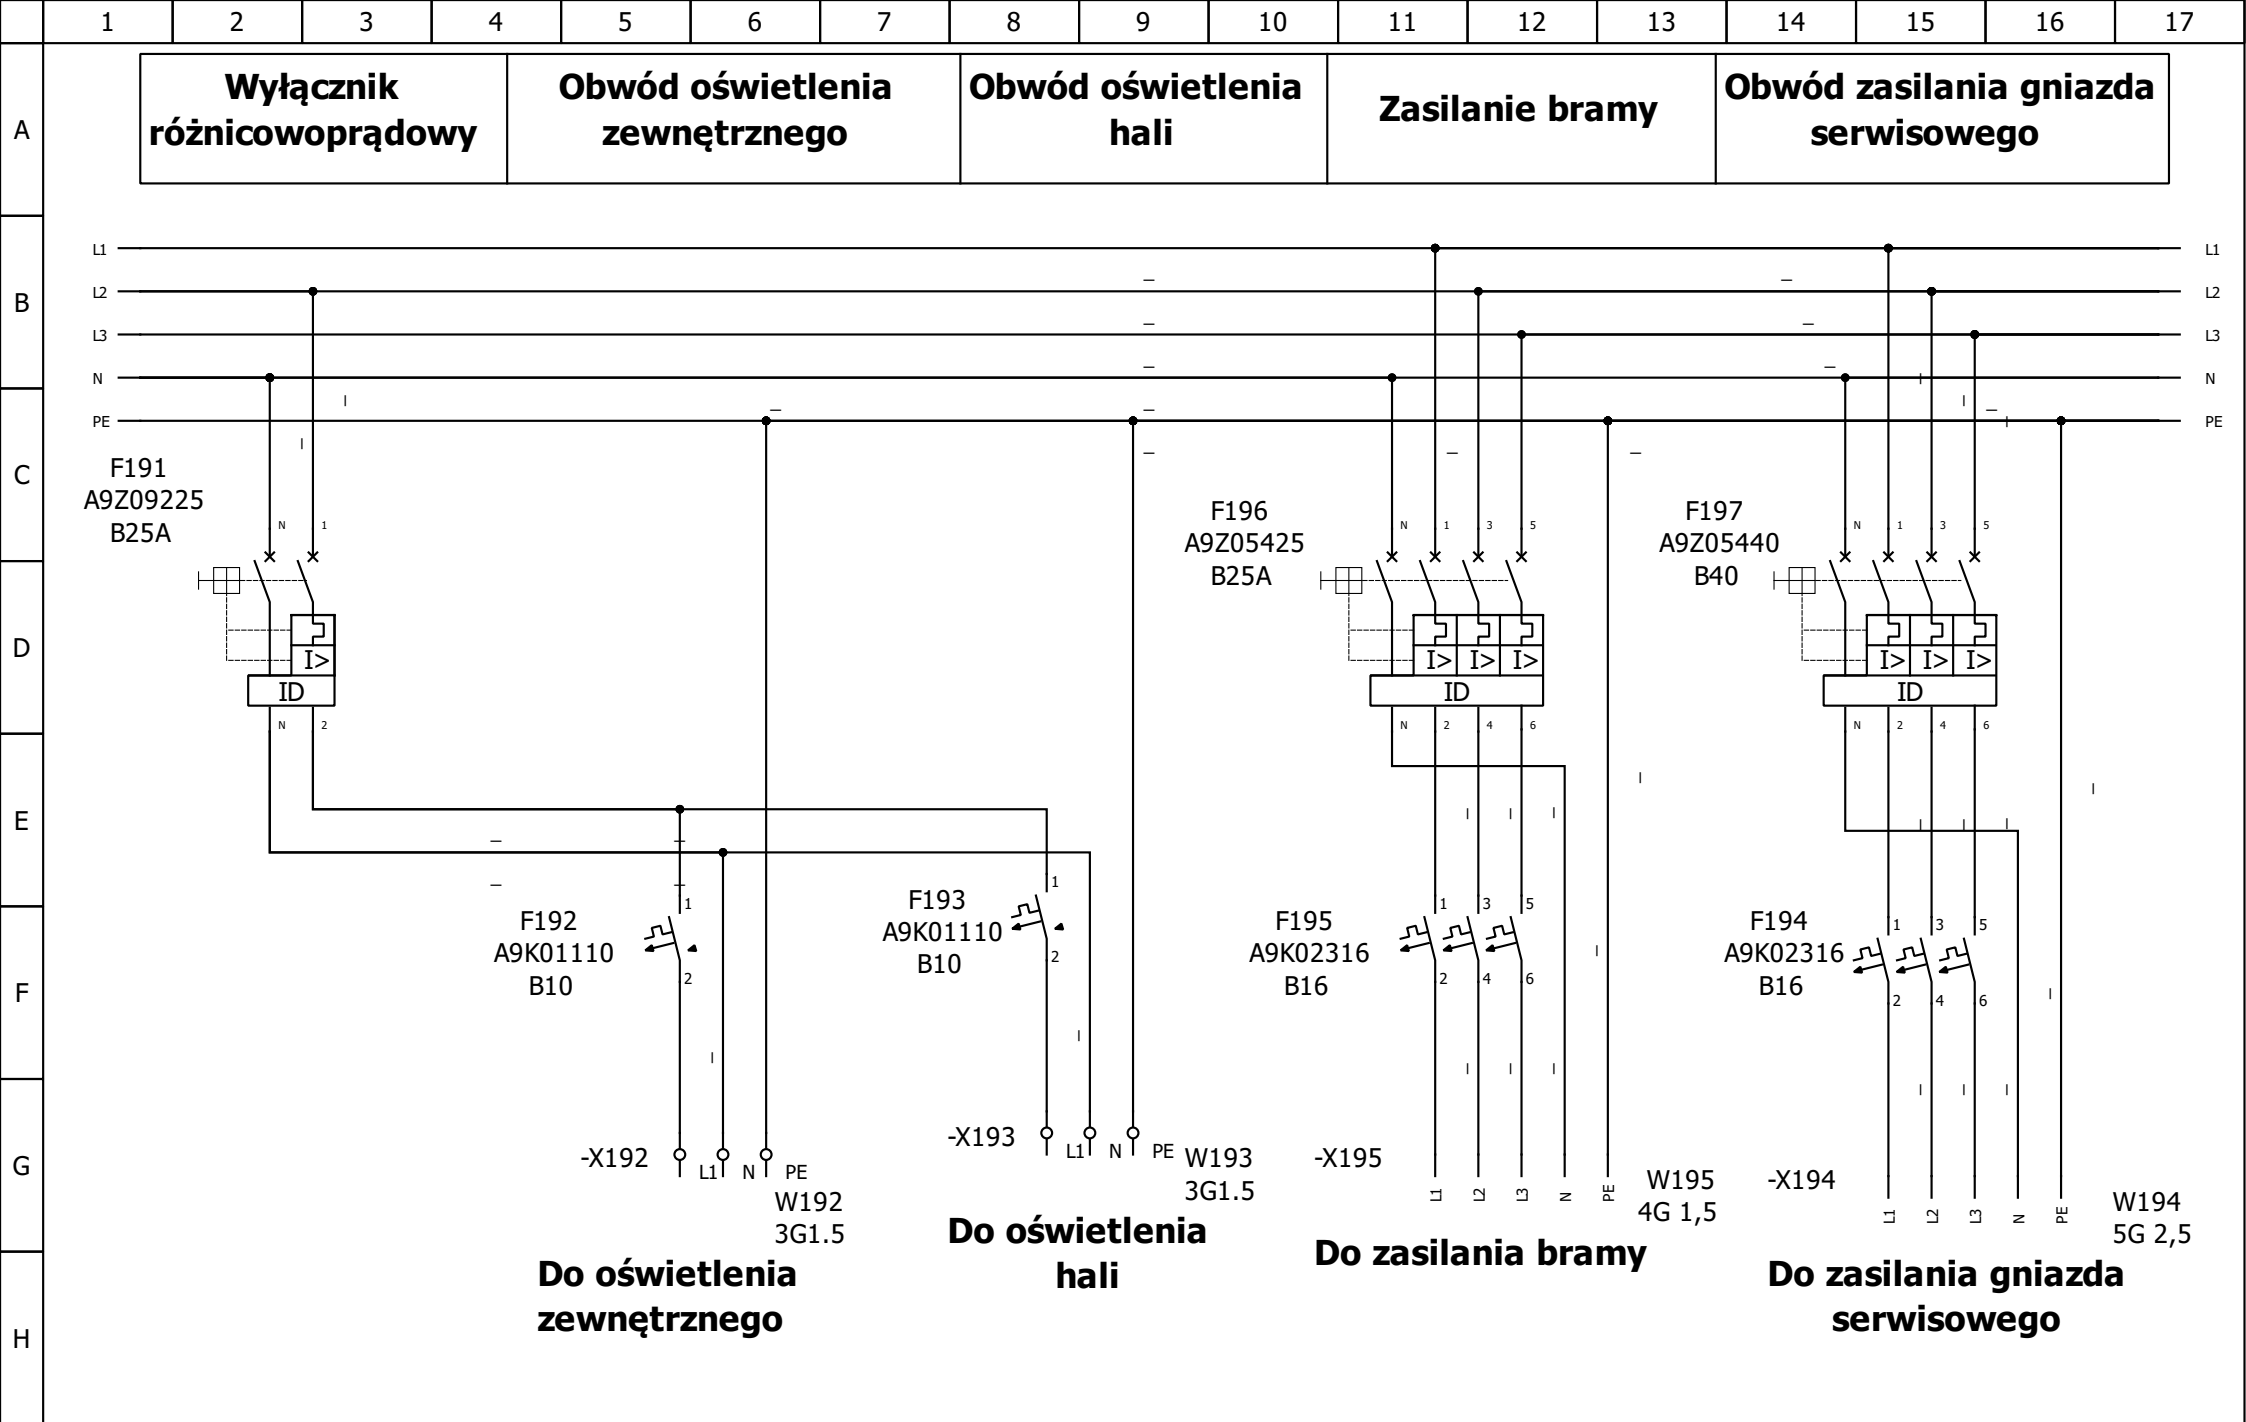


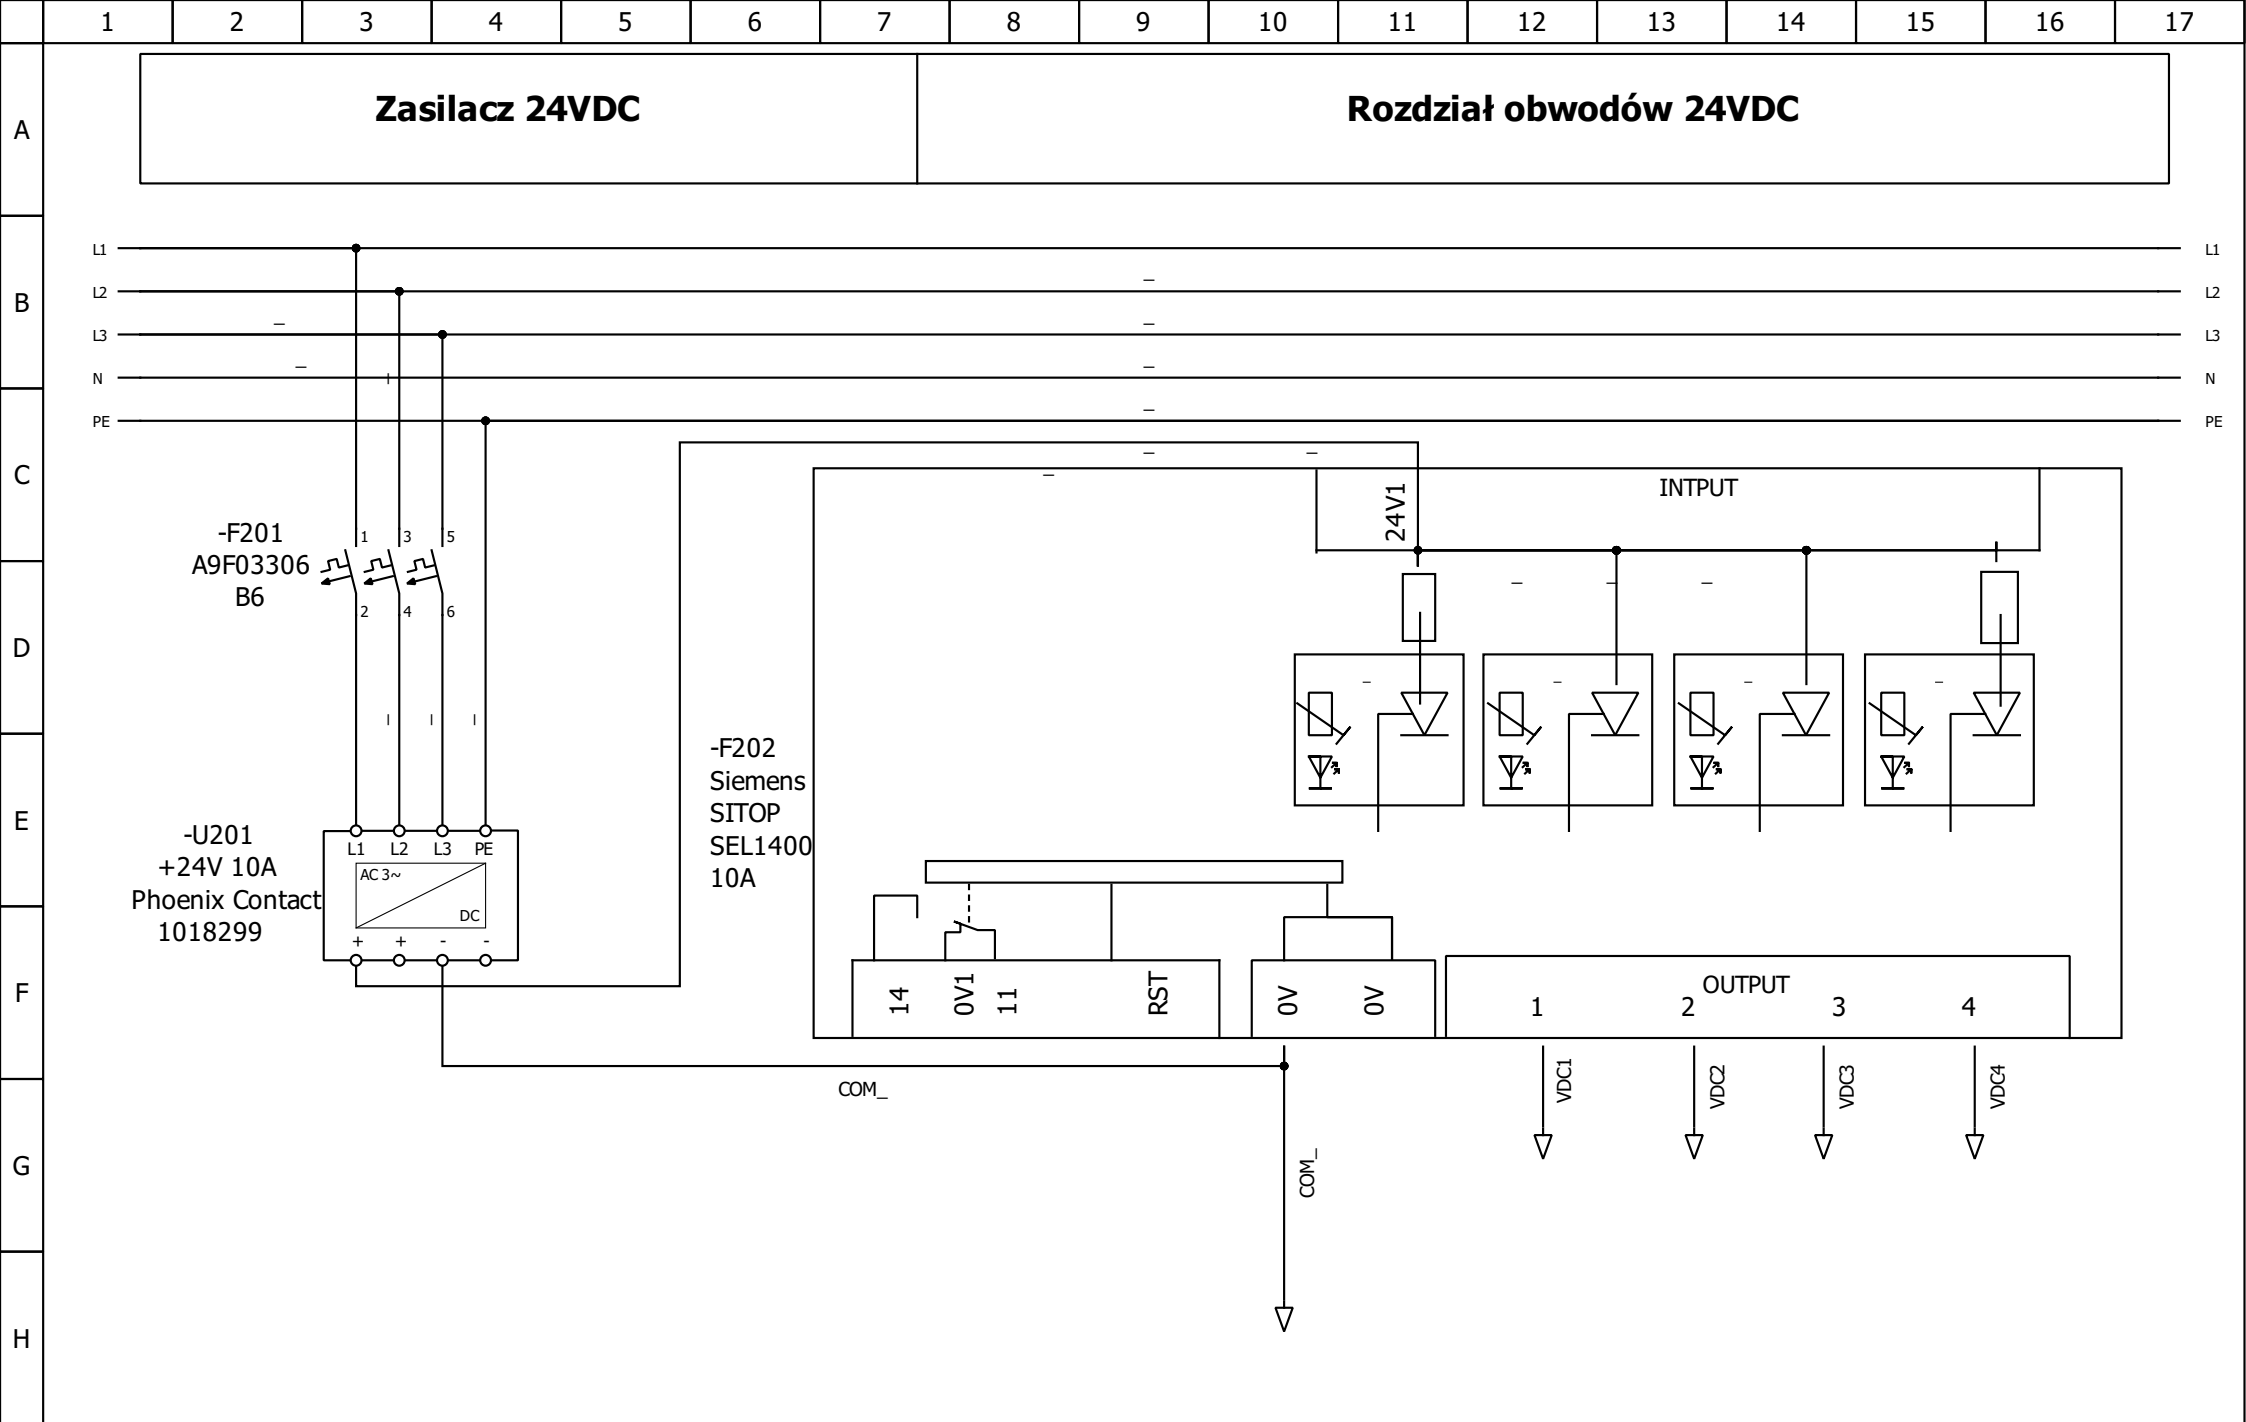

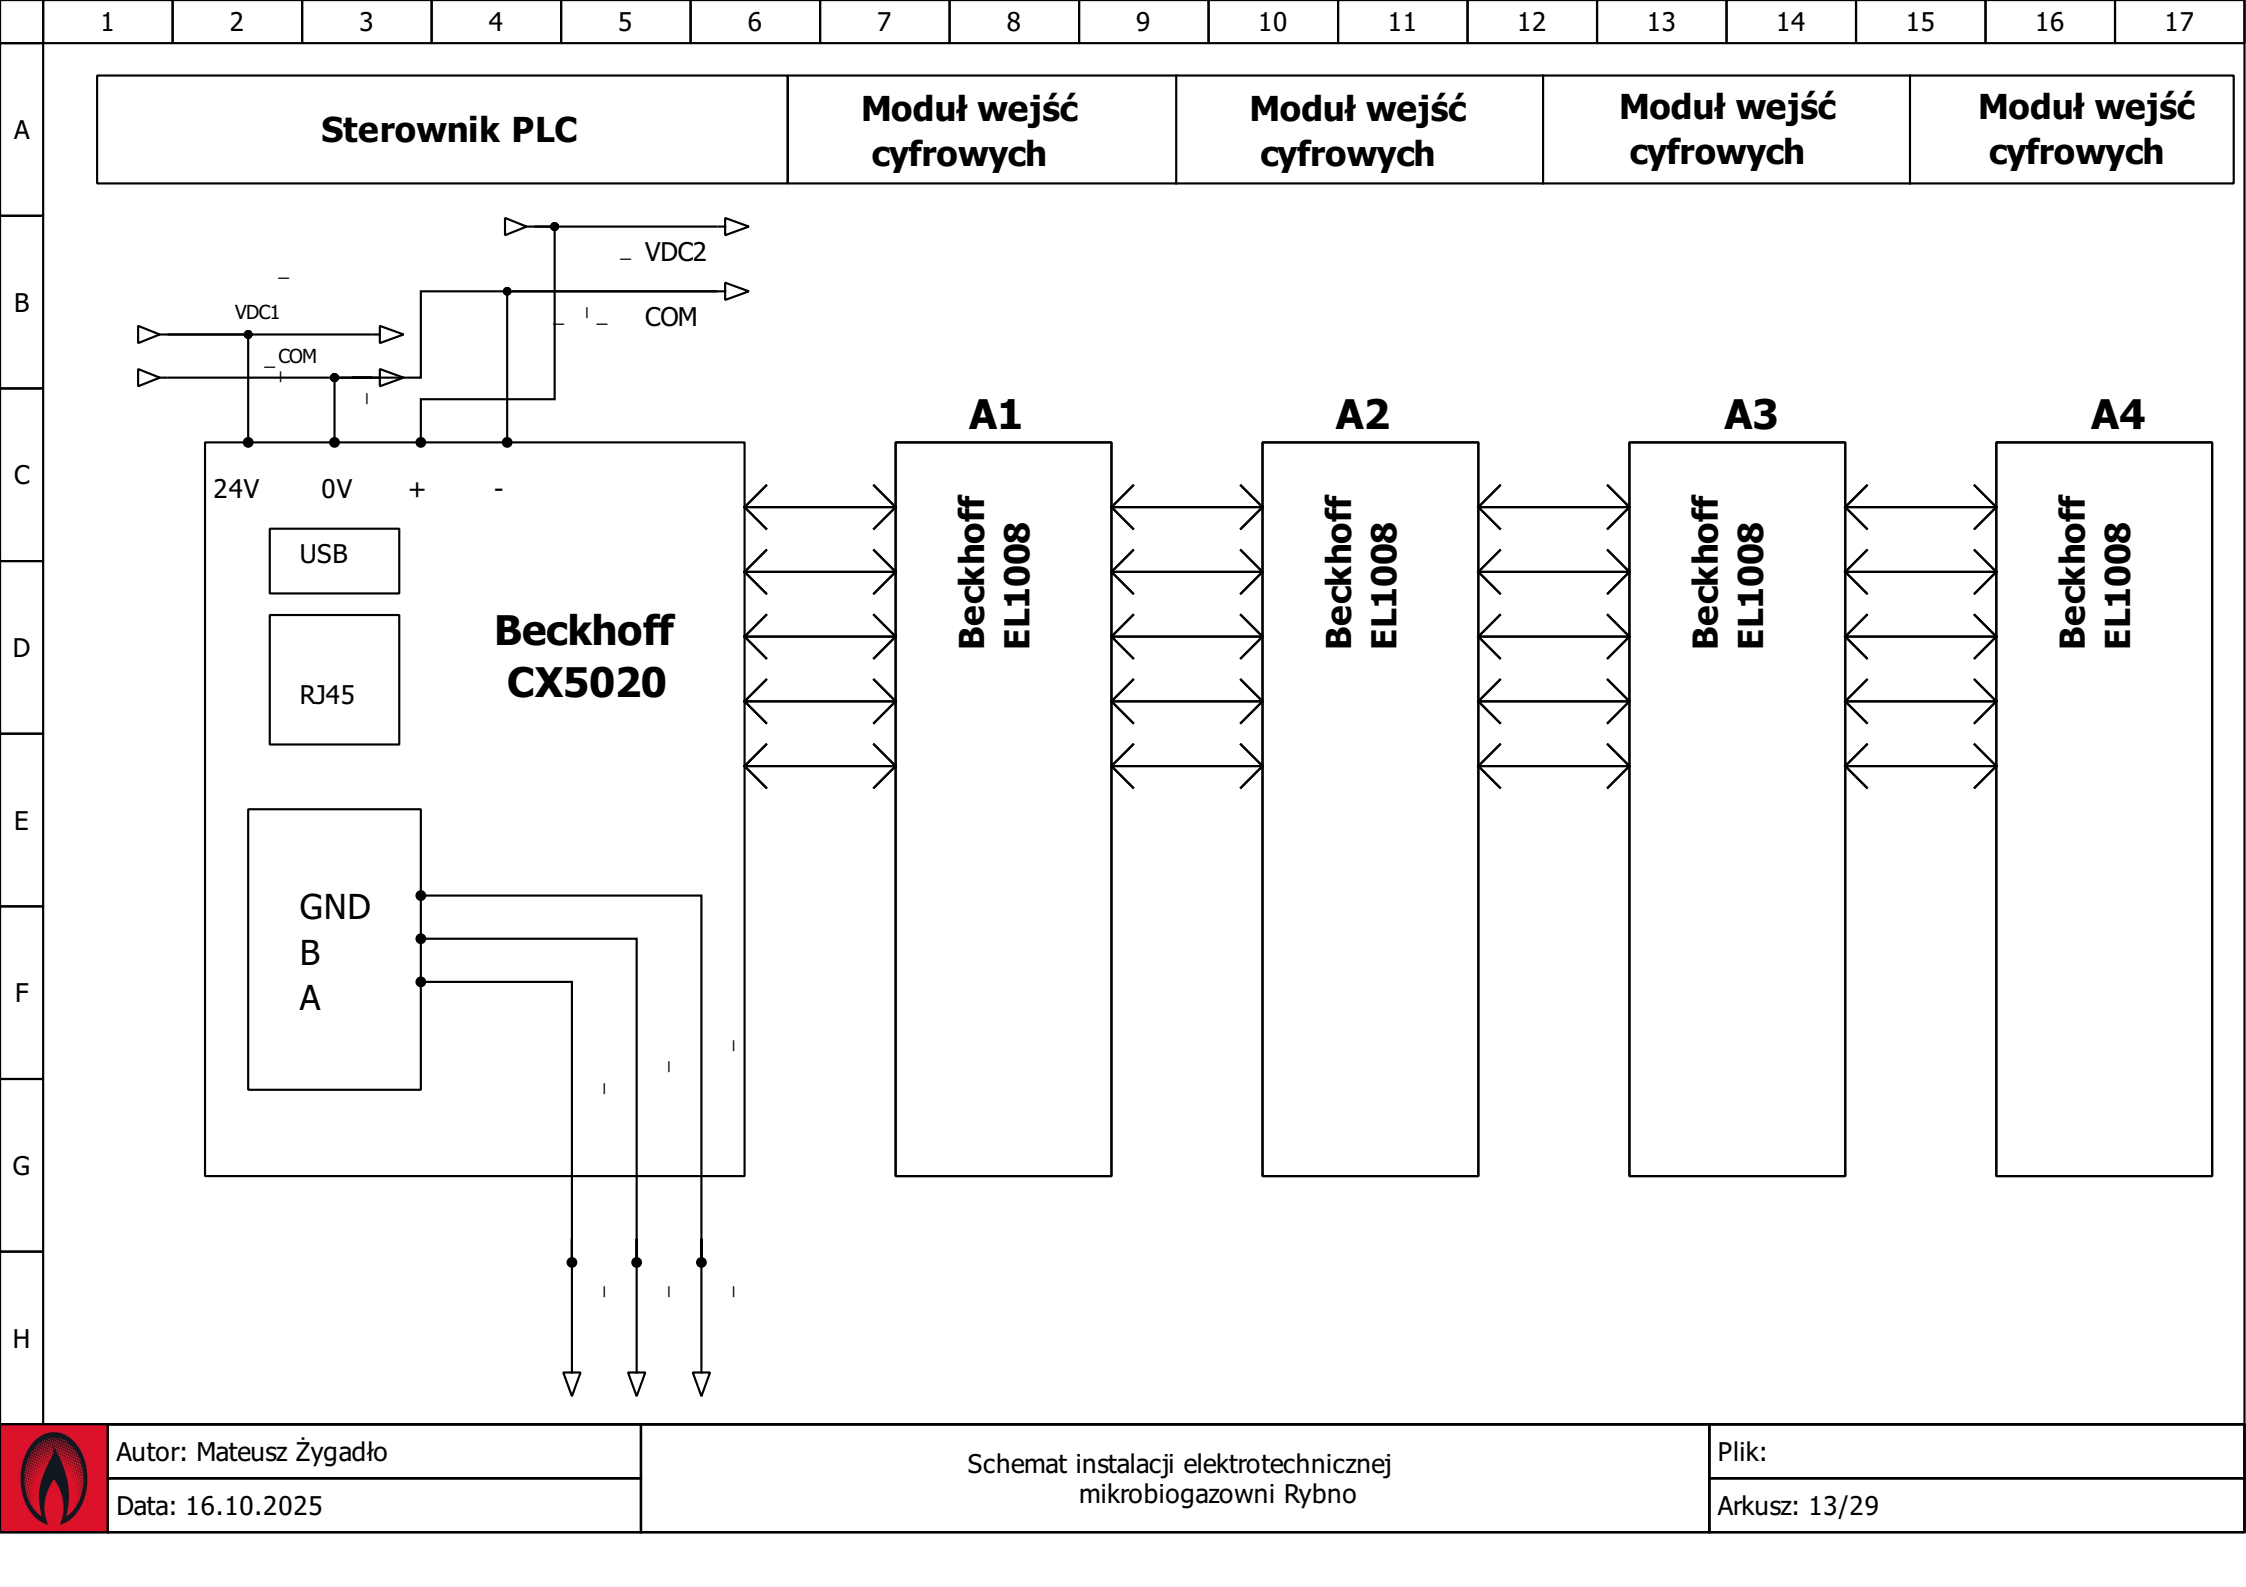


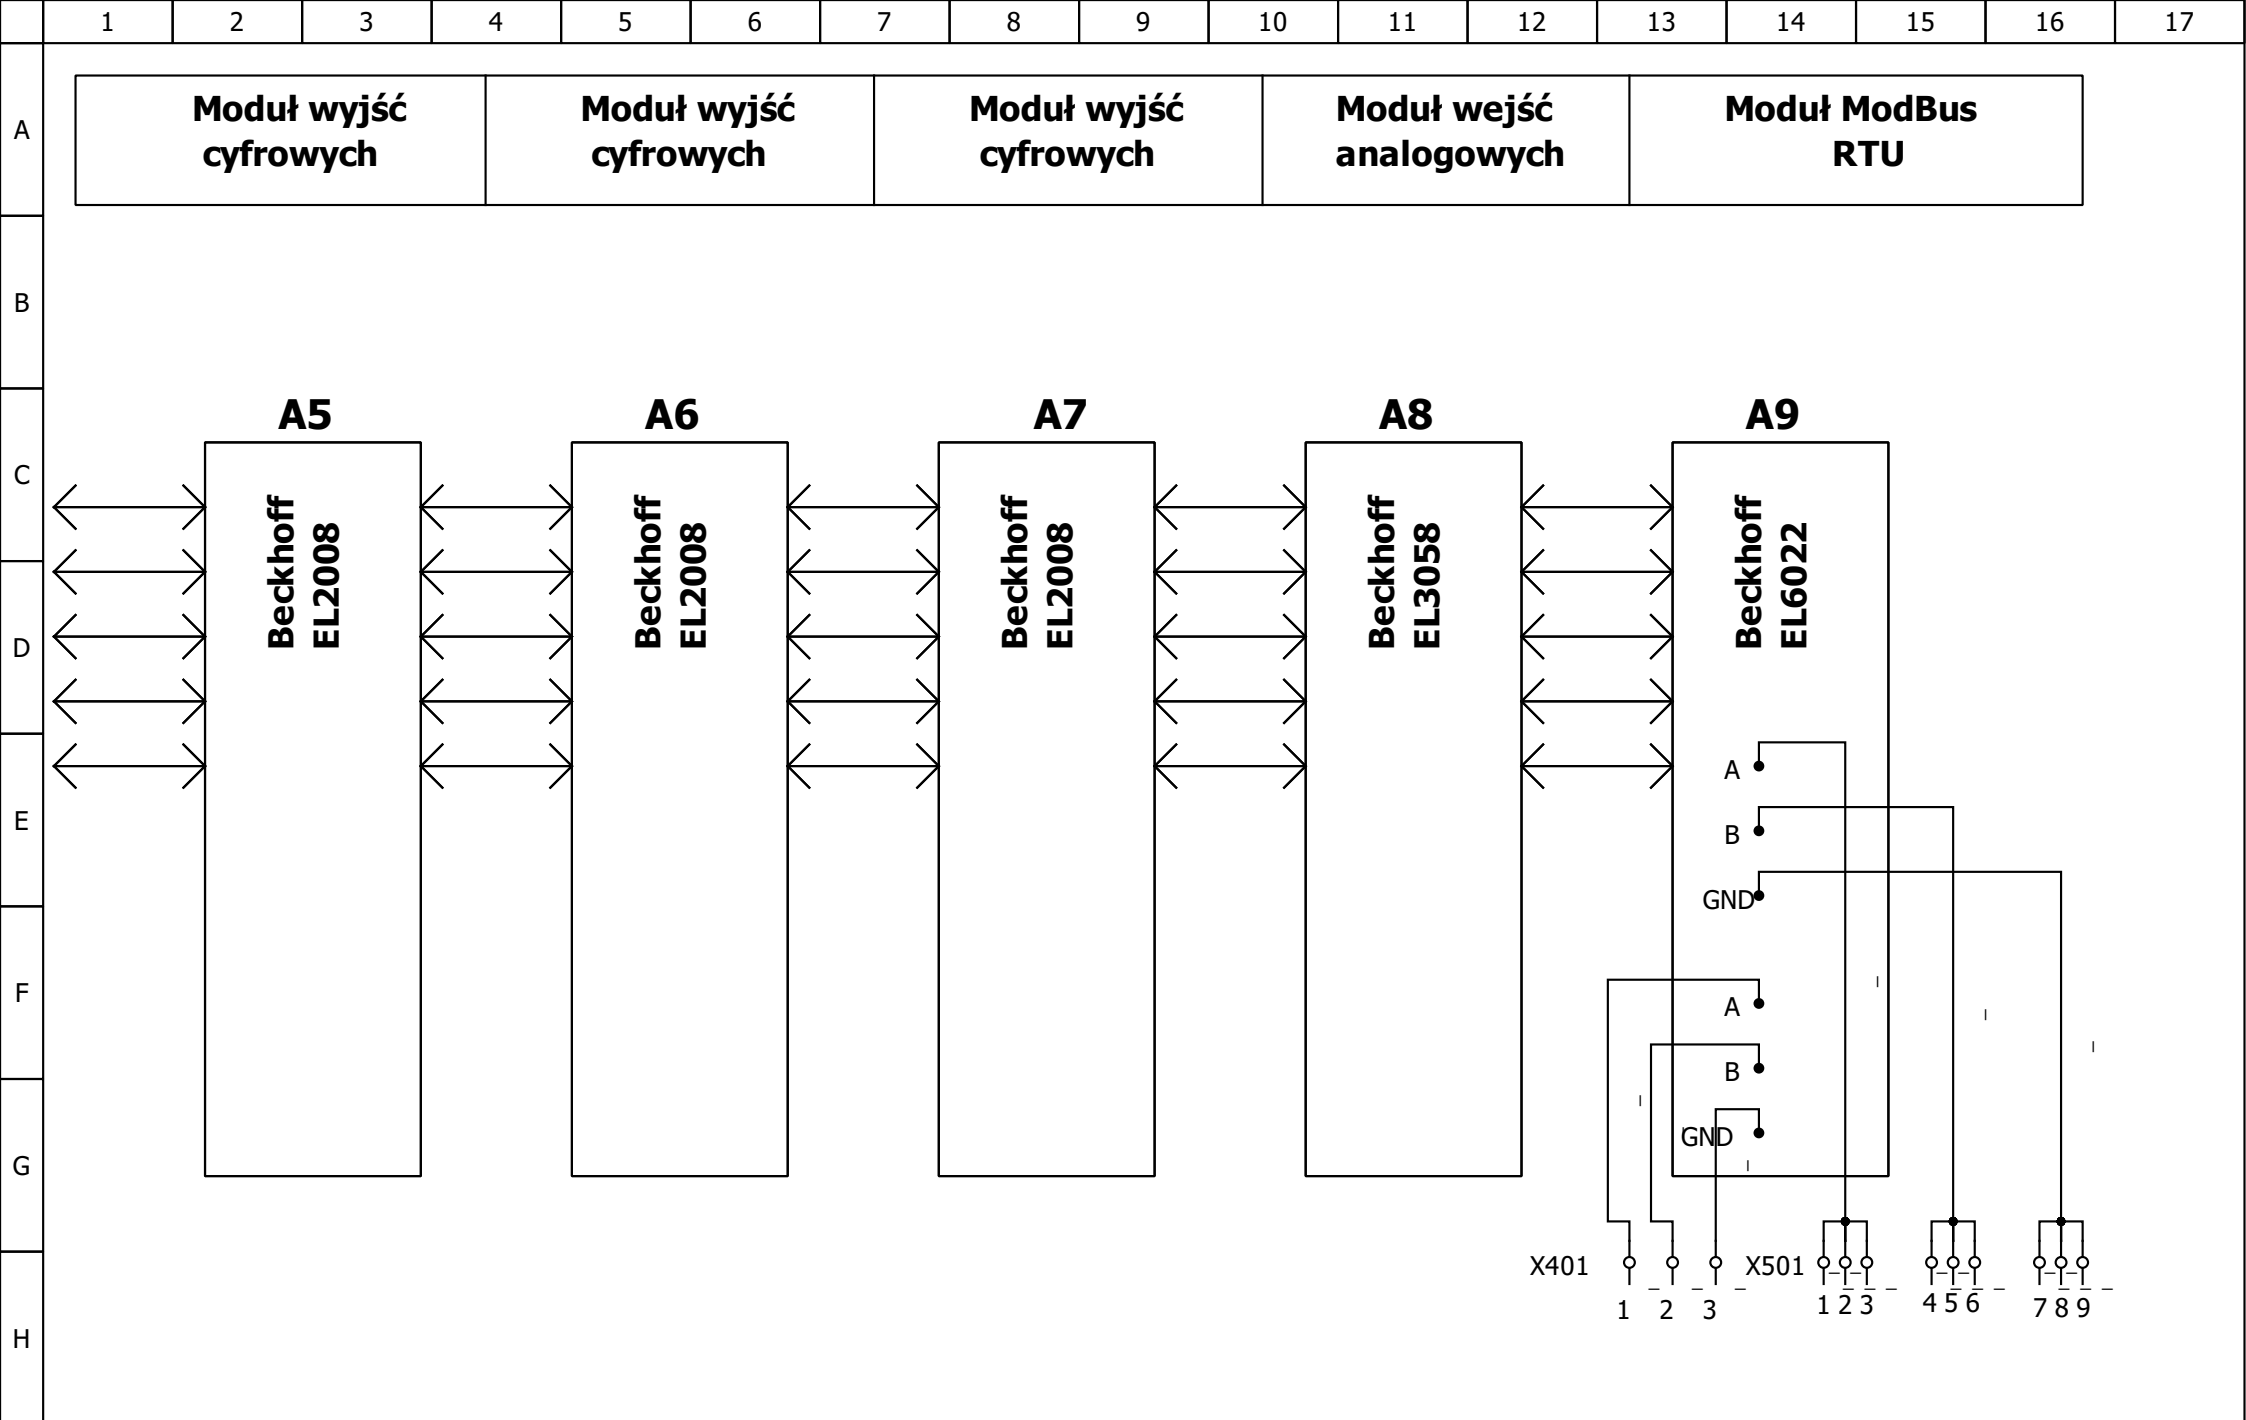


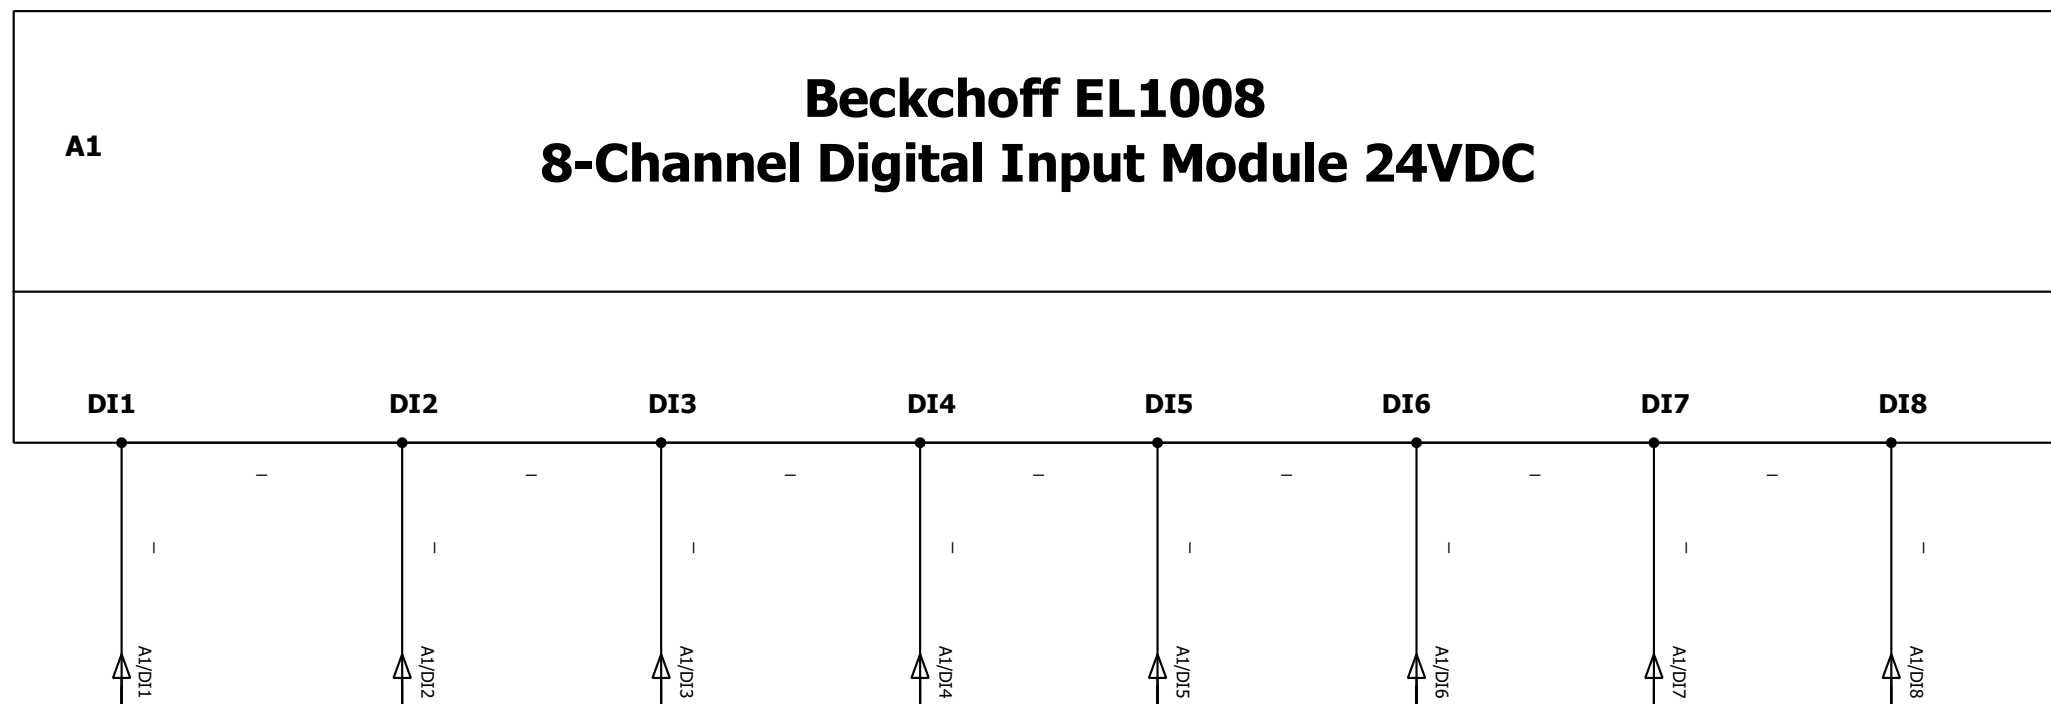

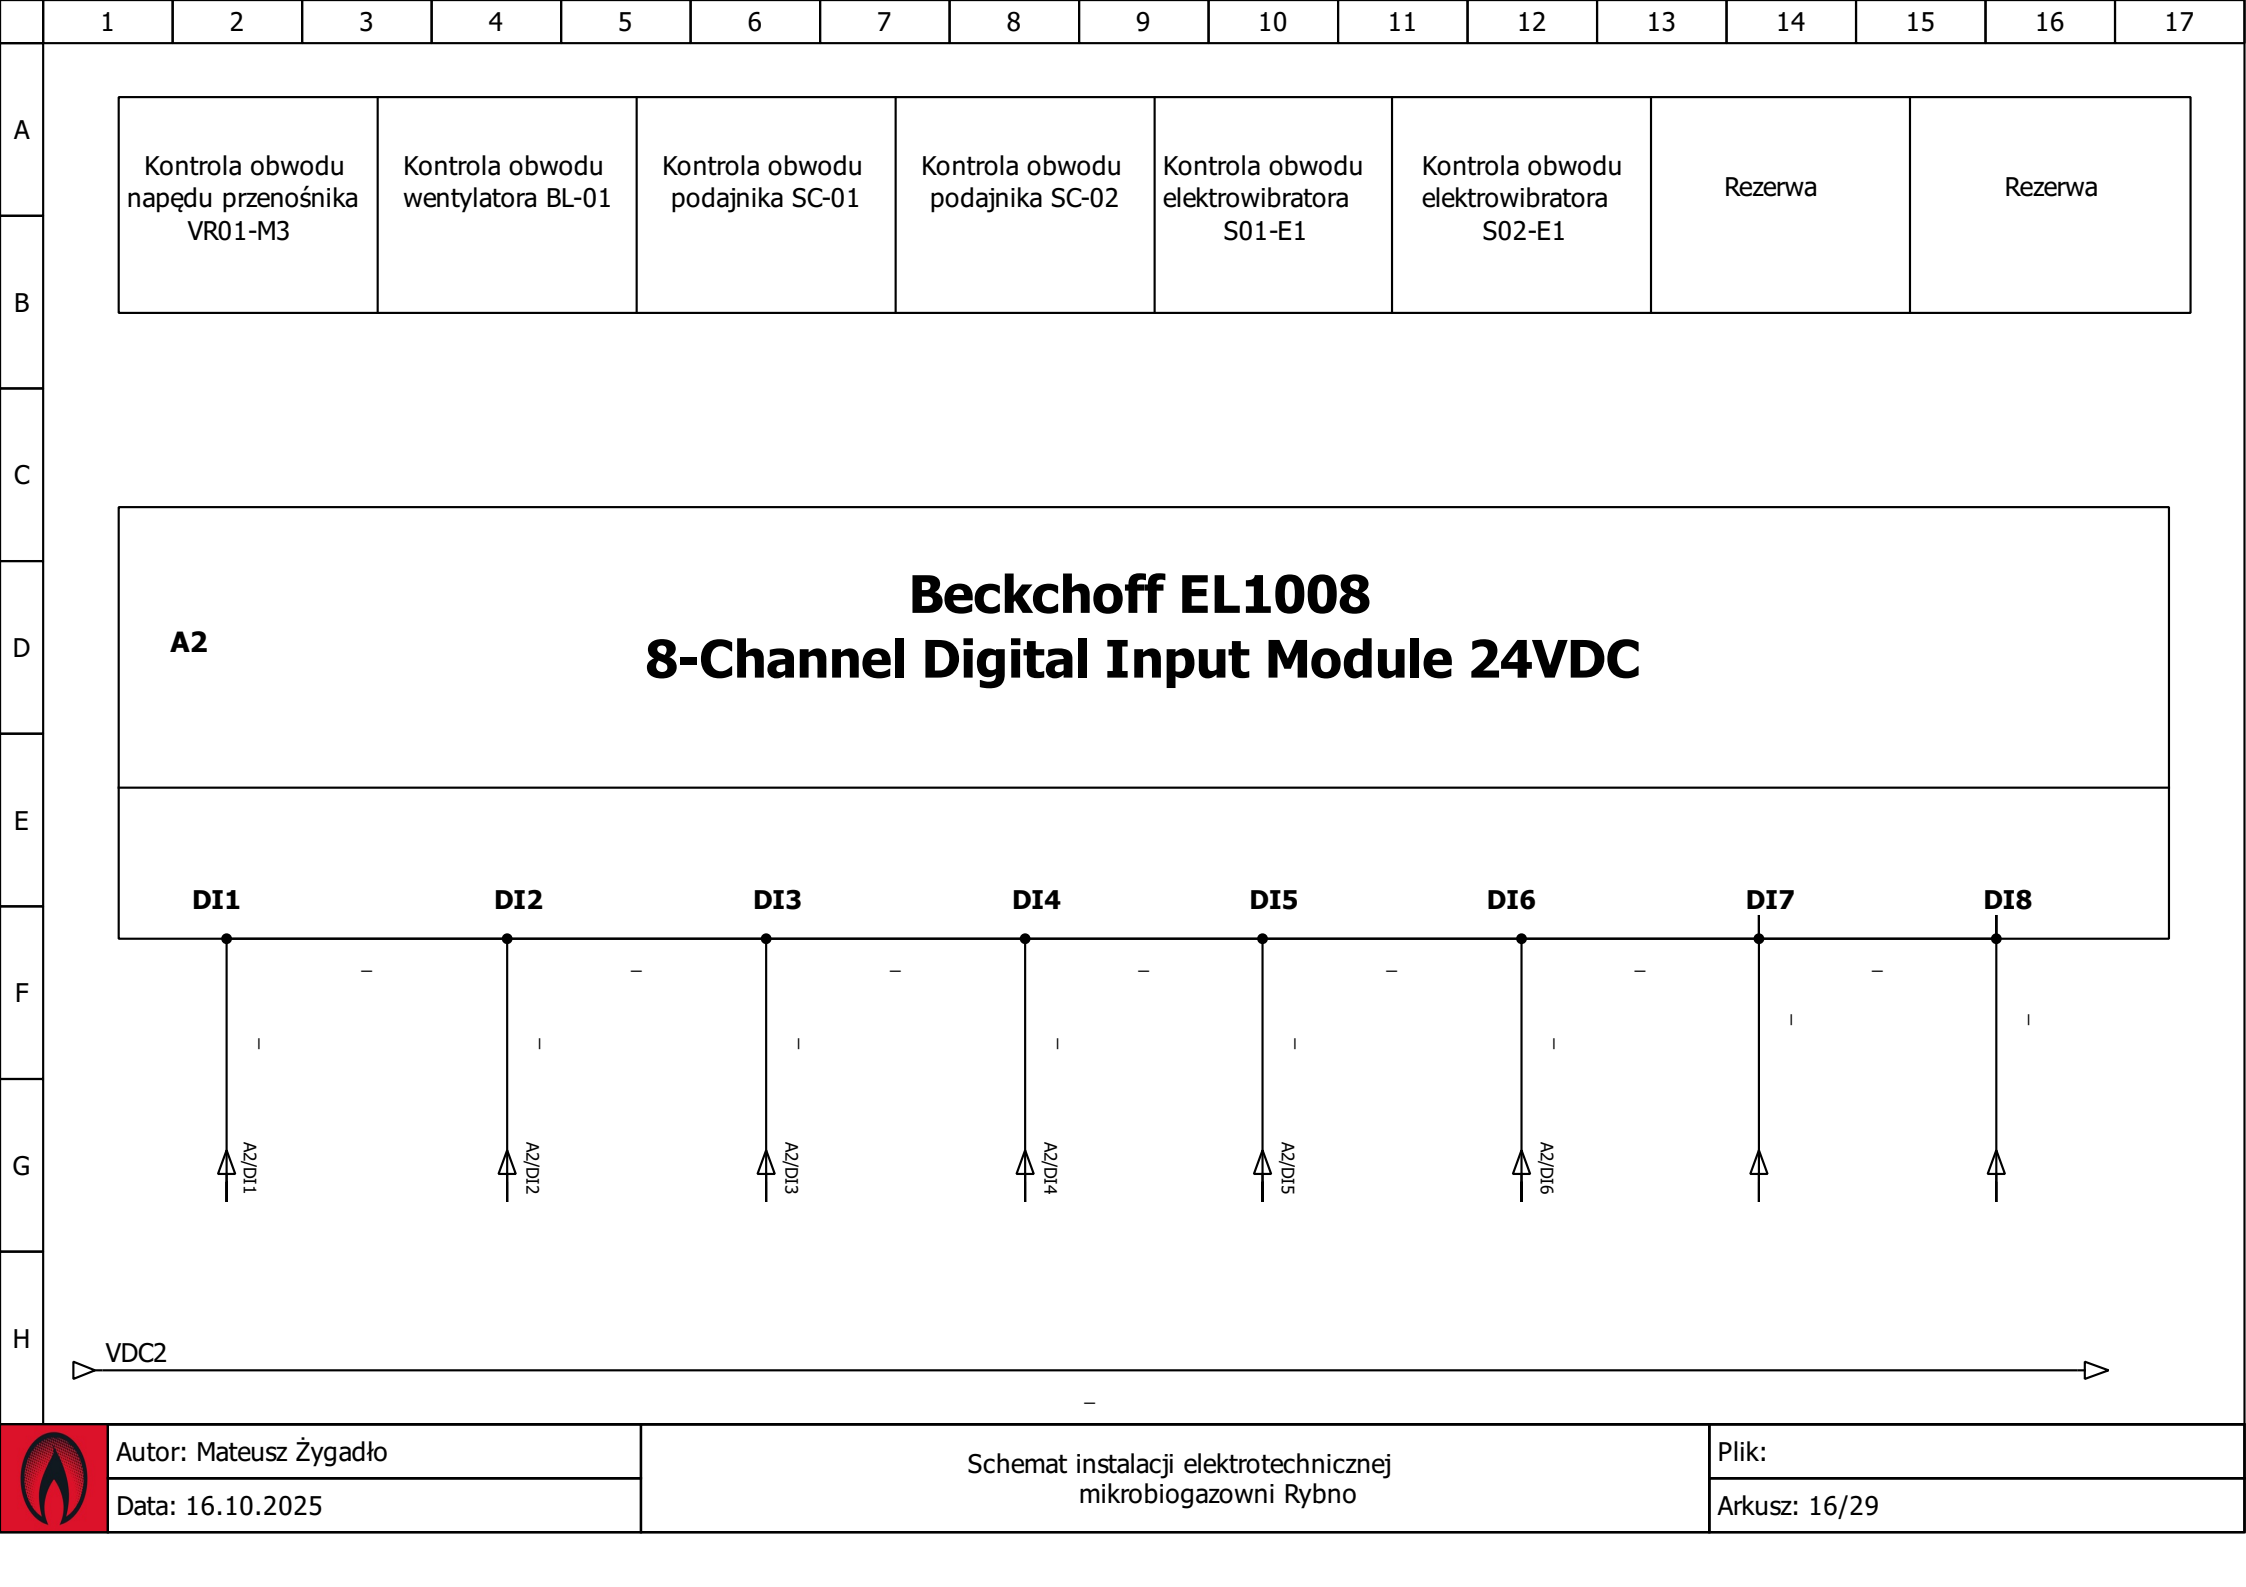

A																
B																

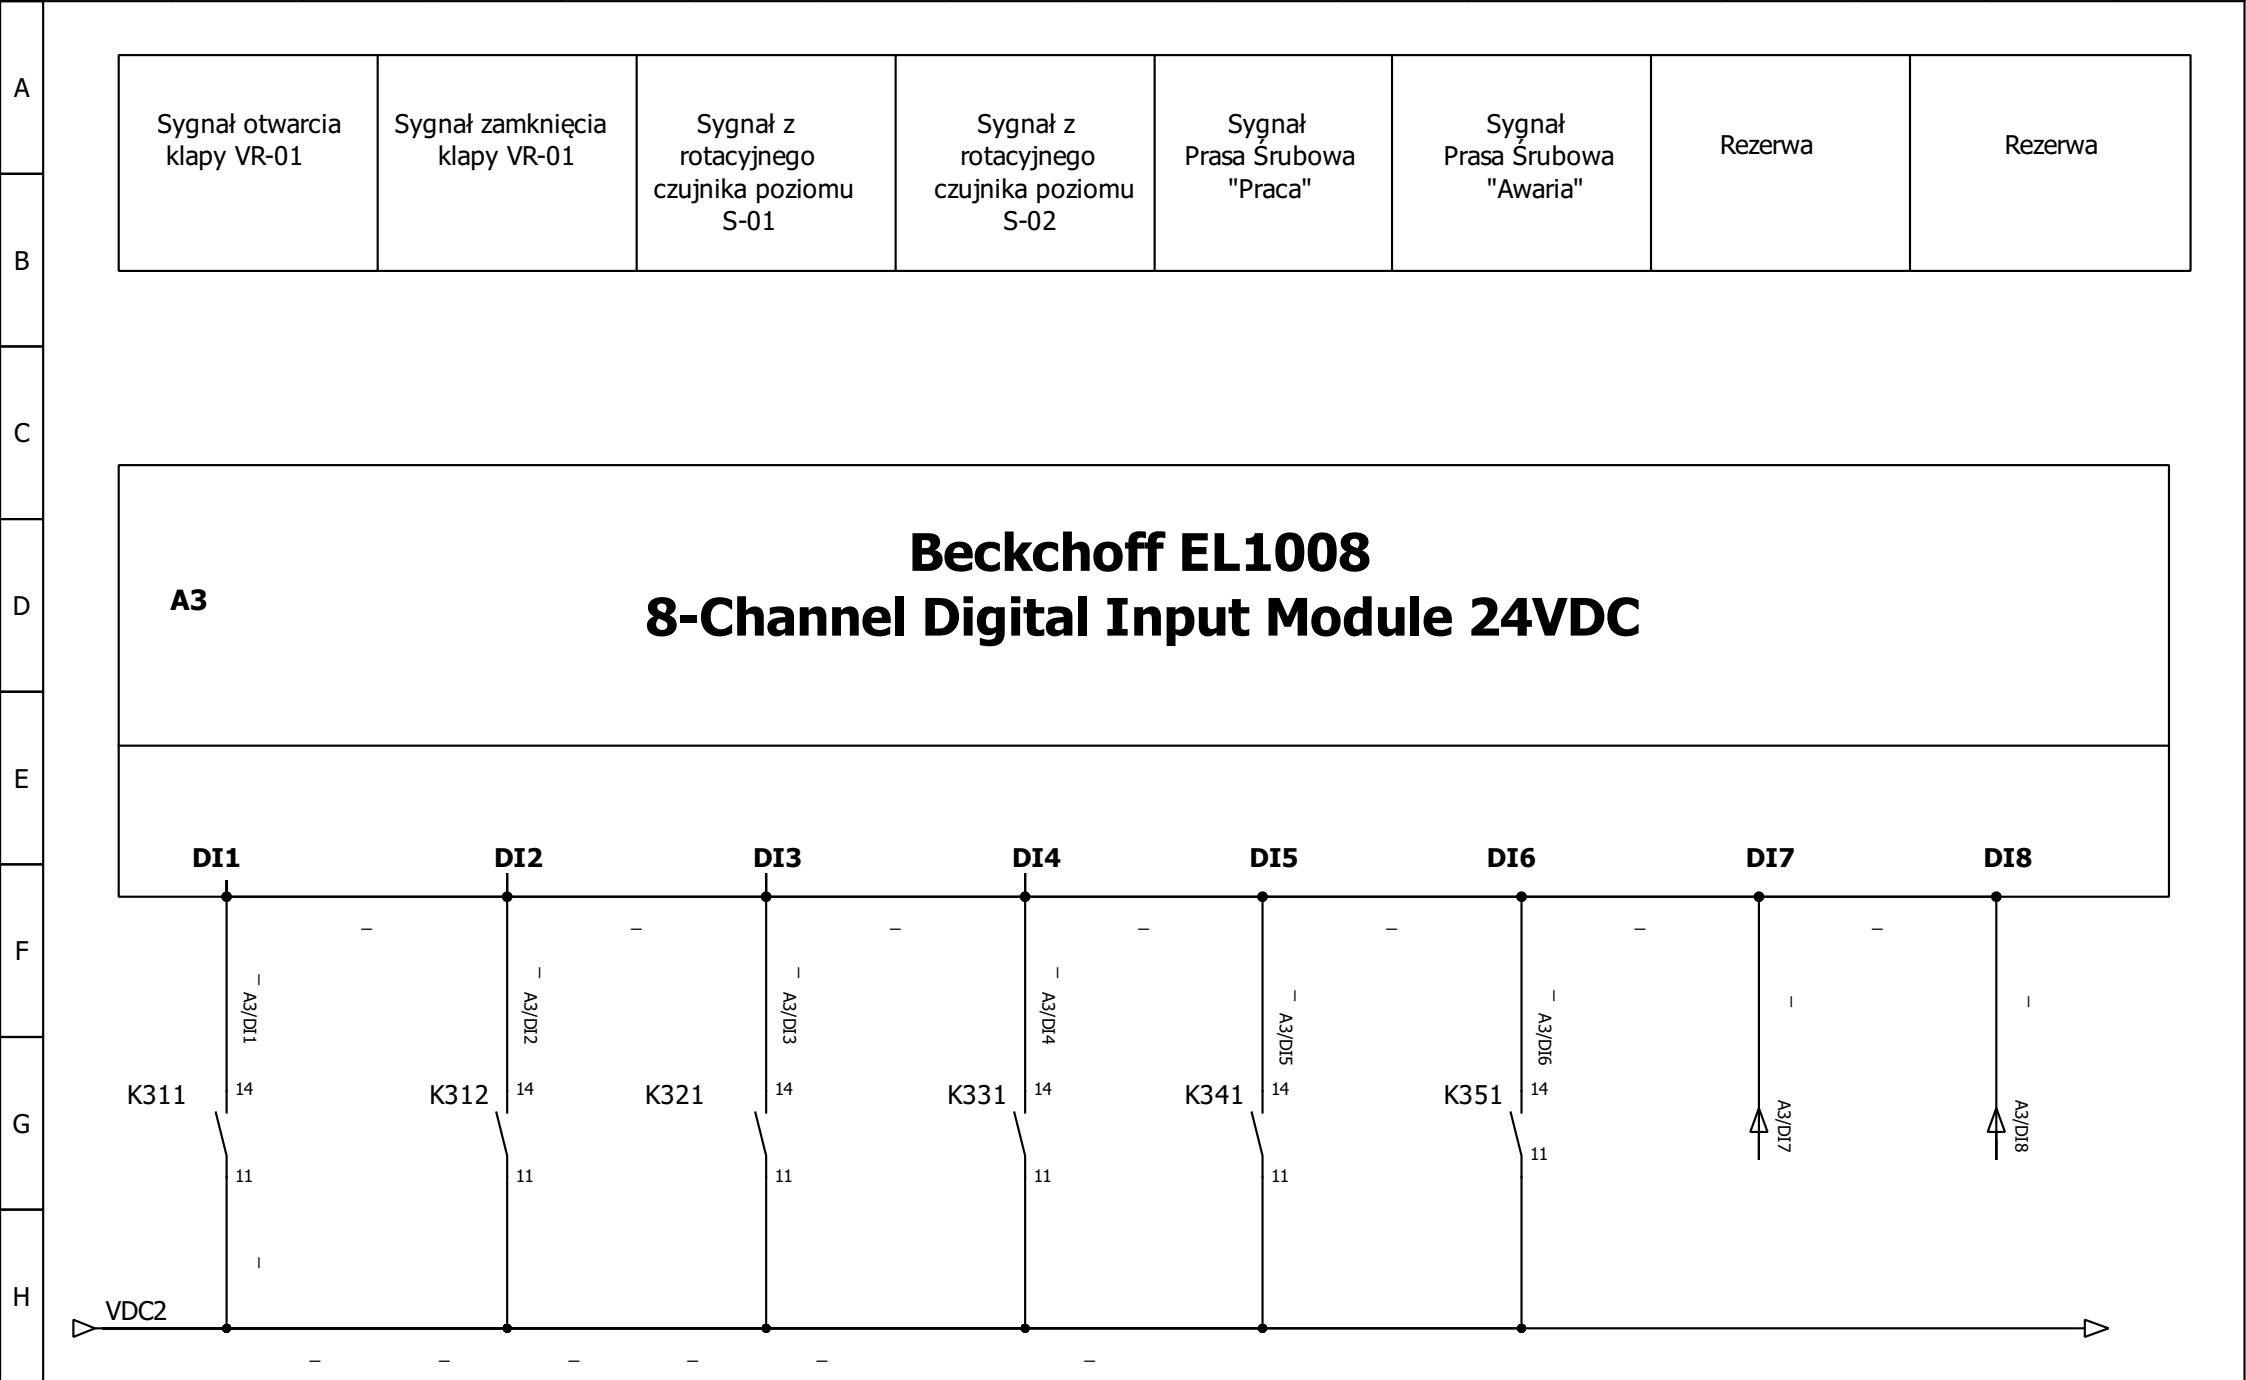

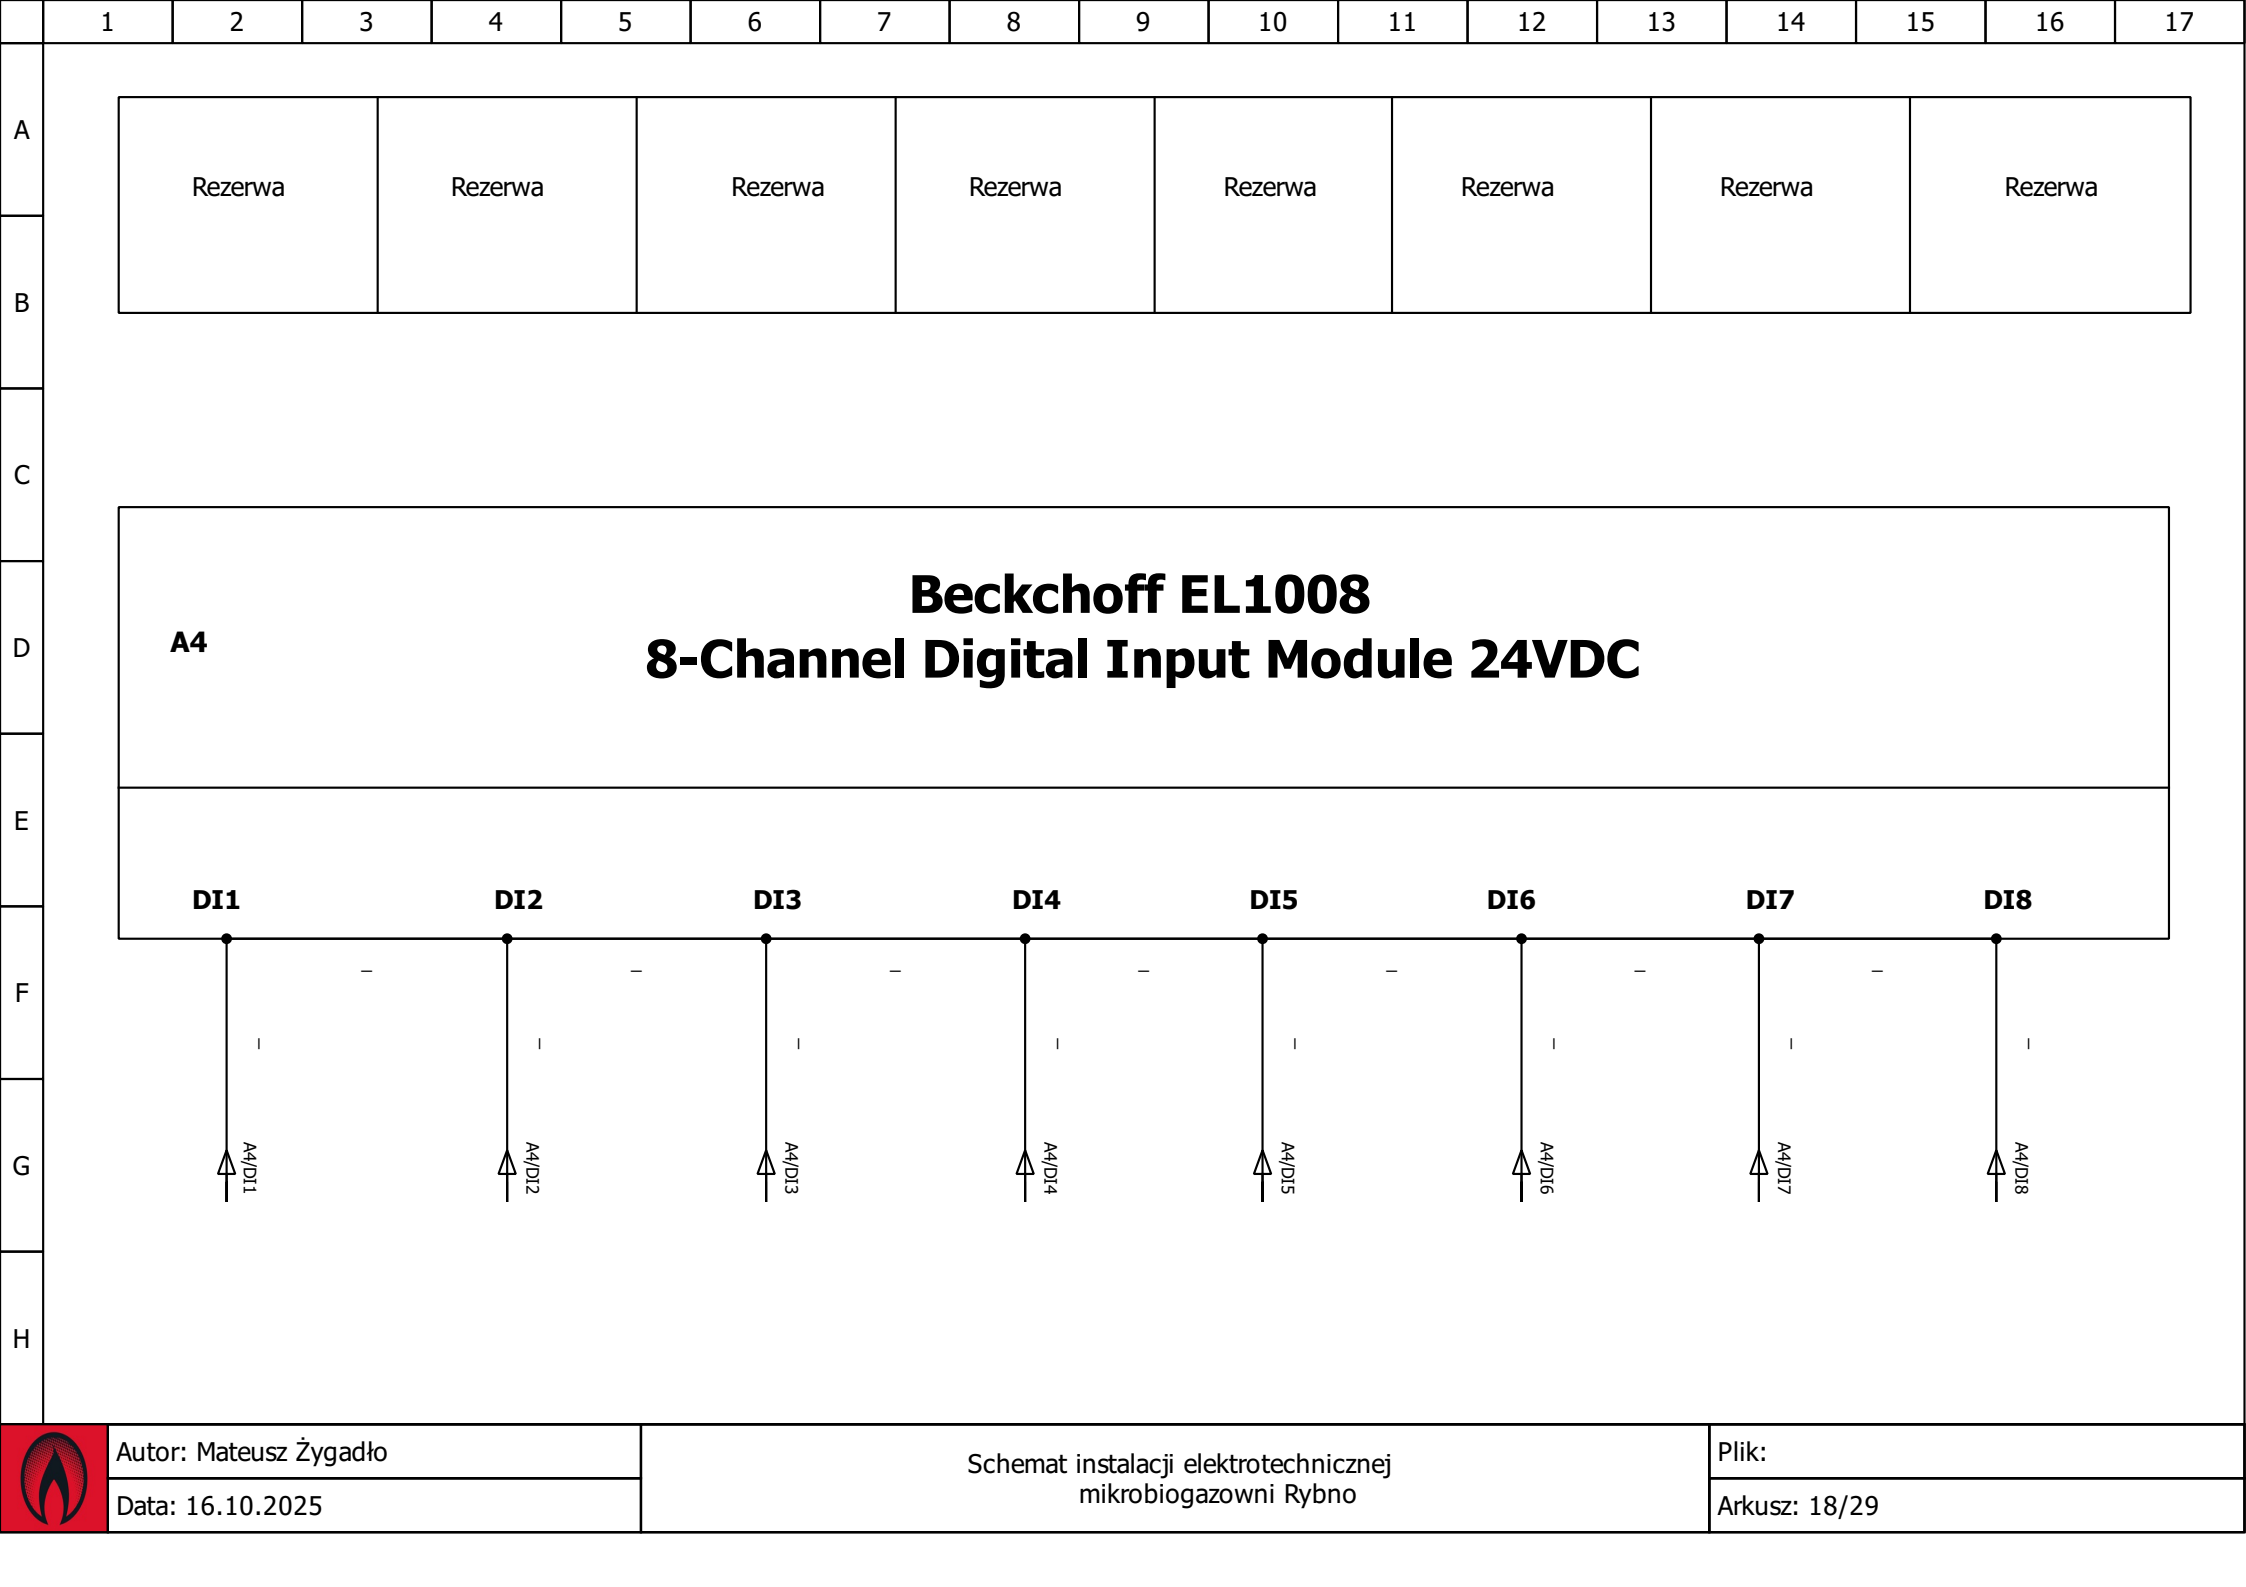

	Autor: Mateusz Żygadło	Schemat instalacji elektrotechnicznej mikrobiogazowni Rybno	Plik:
	Data: 16.10.2025		Arkusz: 18/29

